SITUAÇÃO PRETENDIDA - UNIFICAÇÃO DAS MATRÍCULAS N° 4.928, N° 17.316, N° 21.994, N° 44.540, N° 13.731, N° 9.748 E N° 25.698

Proprietário/Requerente:
MAXCES CONSTRUTORA E INCORPORADORA LTDA
CNPJ n° 33.542.372/0001-07

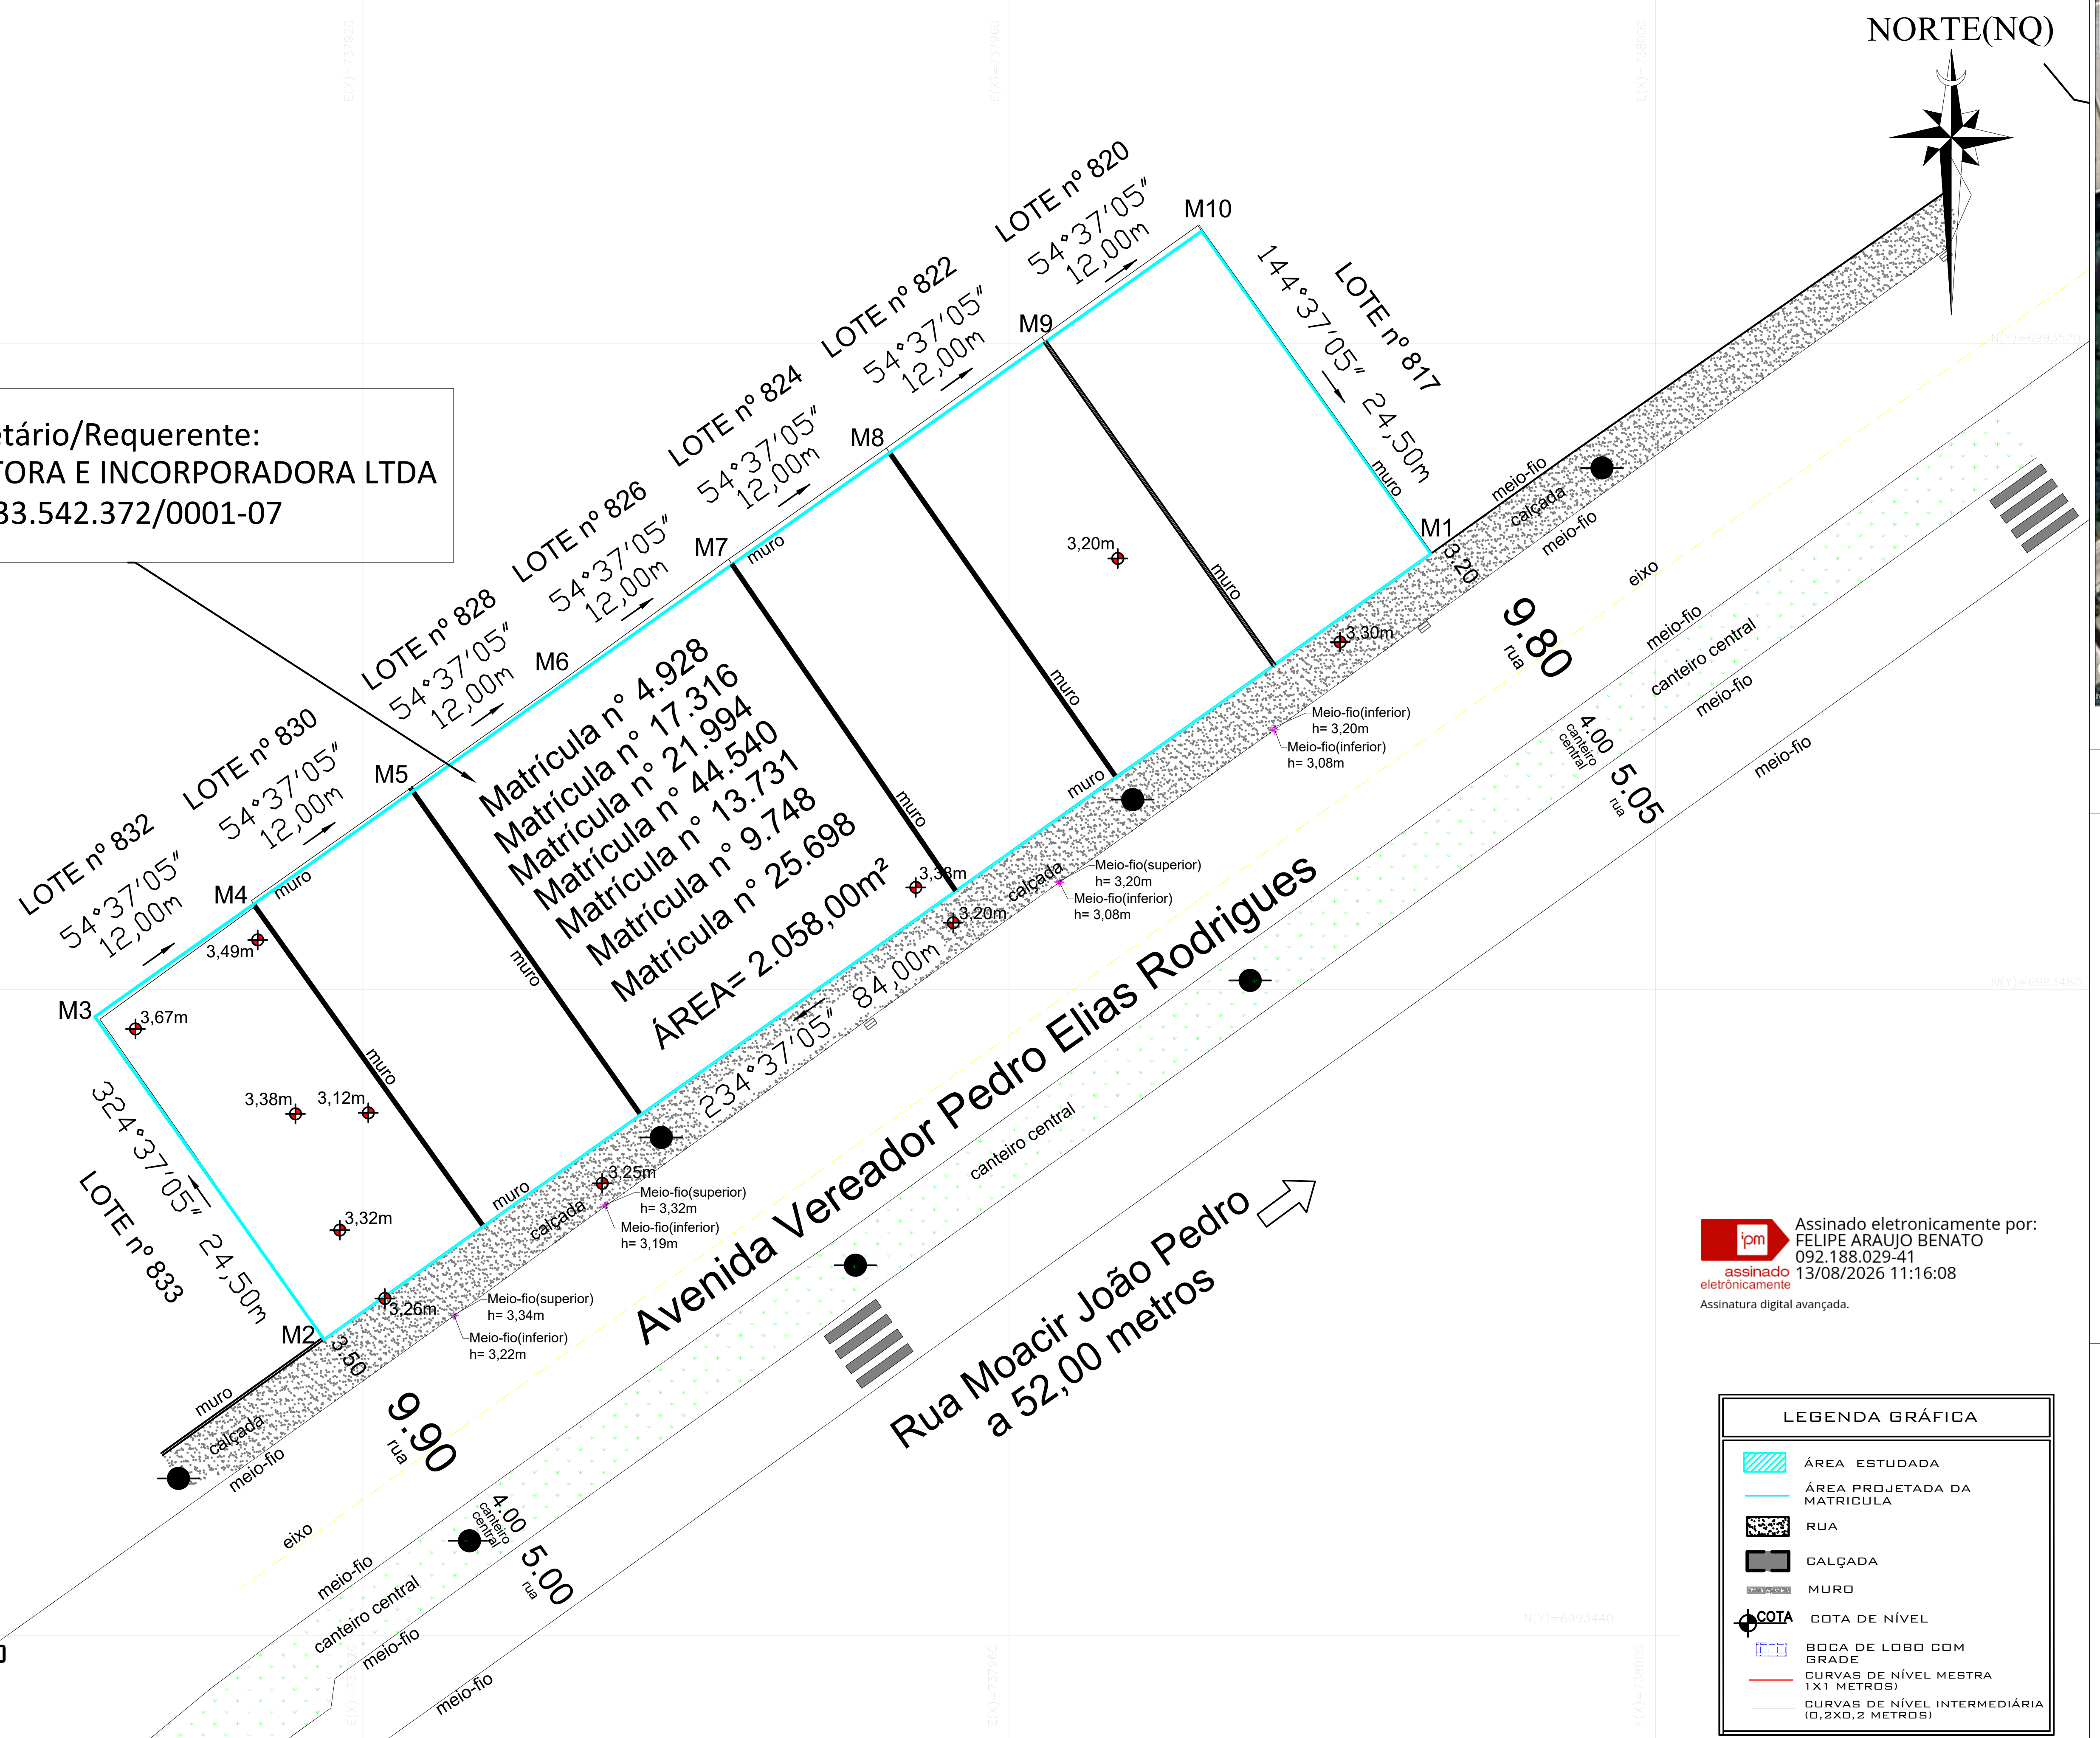

LEVANTAMENTO
TOPOGRÁFICO
PLANIALTIMÉTRICO
ESCALA: 1/400

Assinado eletronicamente por:
FELIPE ARAUJO BENATO
092.188.029-41
13/08/2026 11:16:08
assinado eletrônicamente
Assinatura digital avançada.

LEGENDA GRÁFICA

▨	ÁREA ESTUDADA
—	ÁREA PROJETADA DA MATRICULA
▩	RUA
▬	CALÇADA
▭	MURO
⊕ COTA	COTA DE NÍVEL
▭	BOCA DE LOBO COM GRADE
—	CURVAS DE NÍVEL MESTRA 1X1 METROS)
—	CURVAS DE NÍVEL INTERMEDIÁRIA (0,2X0,2 METROS)

IMAGEM AÉREA - GOOGLE EARTH

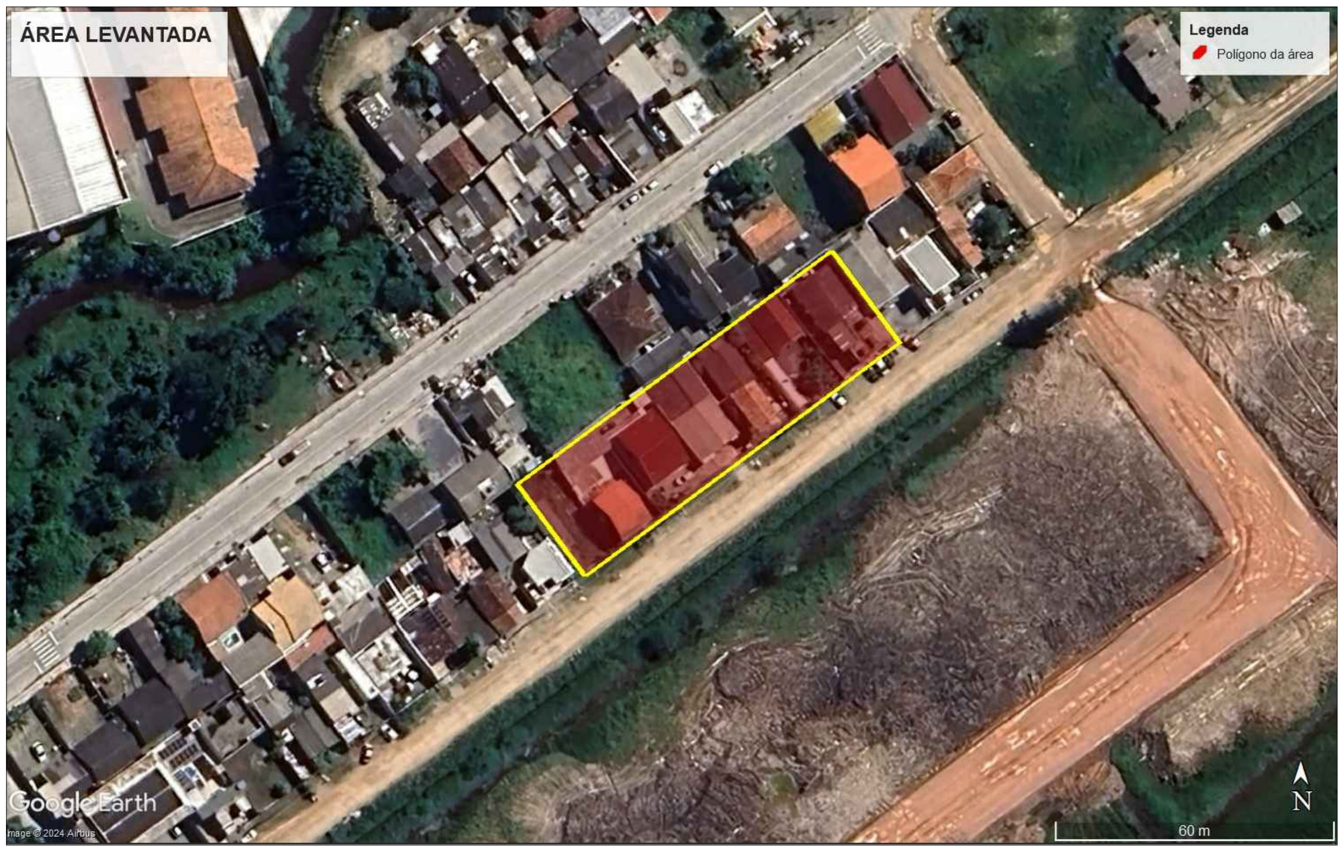

PROJETO DE LOTEAMENTO

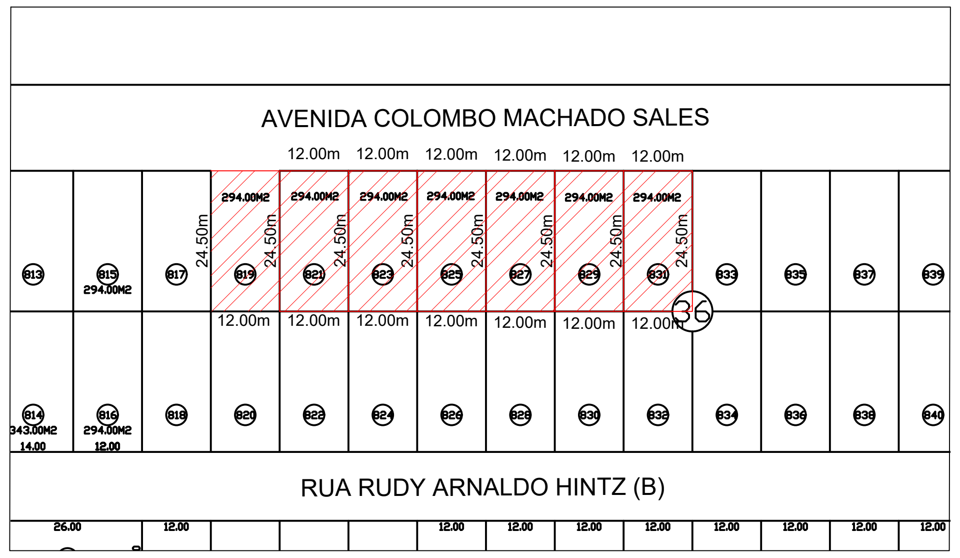

Localização dos lotes N° 819, N° 821, N° 823, N° 825, N° 827, N° 829 e N° 831 no projeto do loteamento "Jardim Dourado", Bairro Perequê - Porto Belo / sc

TABELA DE COORDENADAS UTM (SIRGAS—2000) DE LOCALIZAÇÃO E MEDIDAS UTM DE DISTÂNCIAS E AZIMUTES "IN LOCO"

Vértice	Para	Azimute	Distância	Coord, Norte	Coord, Este	Fator de Escala	Latitude	Longitude
M1	M2	234°37'05"	84,00	6993506,975	737986,101	1,00029551	27°09'37,89625" S	48°35'53,90422" W
M2	M3	324°37'05"	24,50	6993458,337	737917,615	1,00029511	27°09'39,51827" S	48°35'56,35677" W
M3	M4	54°37'05"	12,00	6993478,312	737903,429	1,00029503	27°09'38,87843" S	48°35'56,88566" W
M4	M5	54°37'05"	12,00	6993485,260	737913,213	1,00029508	27°09'38,64672" S	48°35'56,53529" W
M5	M6	54°37'05"	12,00	6993492,209	737922,996	1,00029514	27°09'38,41498" S	48°35'56,18495" W
M6	M7	54°37'05"	12,00	6993499,157	737932,780	1,00029520	27°09'38,18327" S	48°35'55,83457" W
M7	M8	54°37'05"	12,00	6993506,105	737942,564	1,00029525	27°09'37,95156" S	48°35'55,48420" W
M8	M9	54°37'05"	12,00	6993513,054	737952,348	1,00029531	27°09'37,71982" S	48°35'55,13383" W
M9	M10	54°37'05"	12,00	6993520,002	737962,131	1,00029537	27°09'37,48812" S	48°35'54,78349" W
M10	M1	144°37'05"	24,50	6993526,950	737971,915	1,00029543	27°09'37,25641" S	48°35'54,43312" W

Área=2.058,00 m2
Perímetro=217,00 m

ESTE DOCUMENTO FOI ASSINADO EM: 13/08/2026 11:16 -03:00 -03
PARA CONFERÊNCIA DO SEU CONTEÚDO ACESSE: https://c.ipm.com.br/pebf6a643005f1

SITUAÇÃO ATUAL - CONFORME MATRÍCULAS N° 4.928, N° 17.316, N° 21.994, N° 44.540, N° 13.731, N° 9.748 E N° 25.698

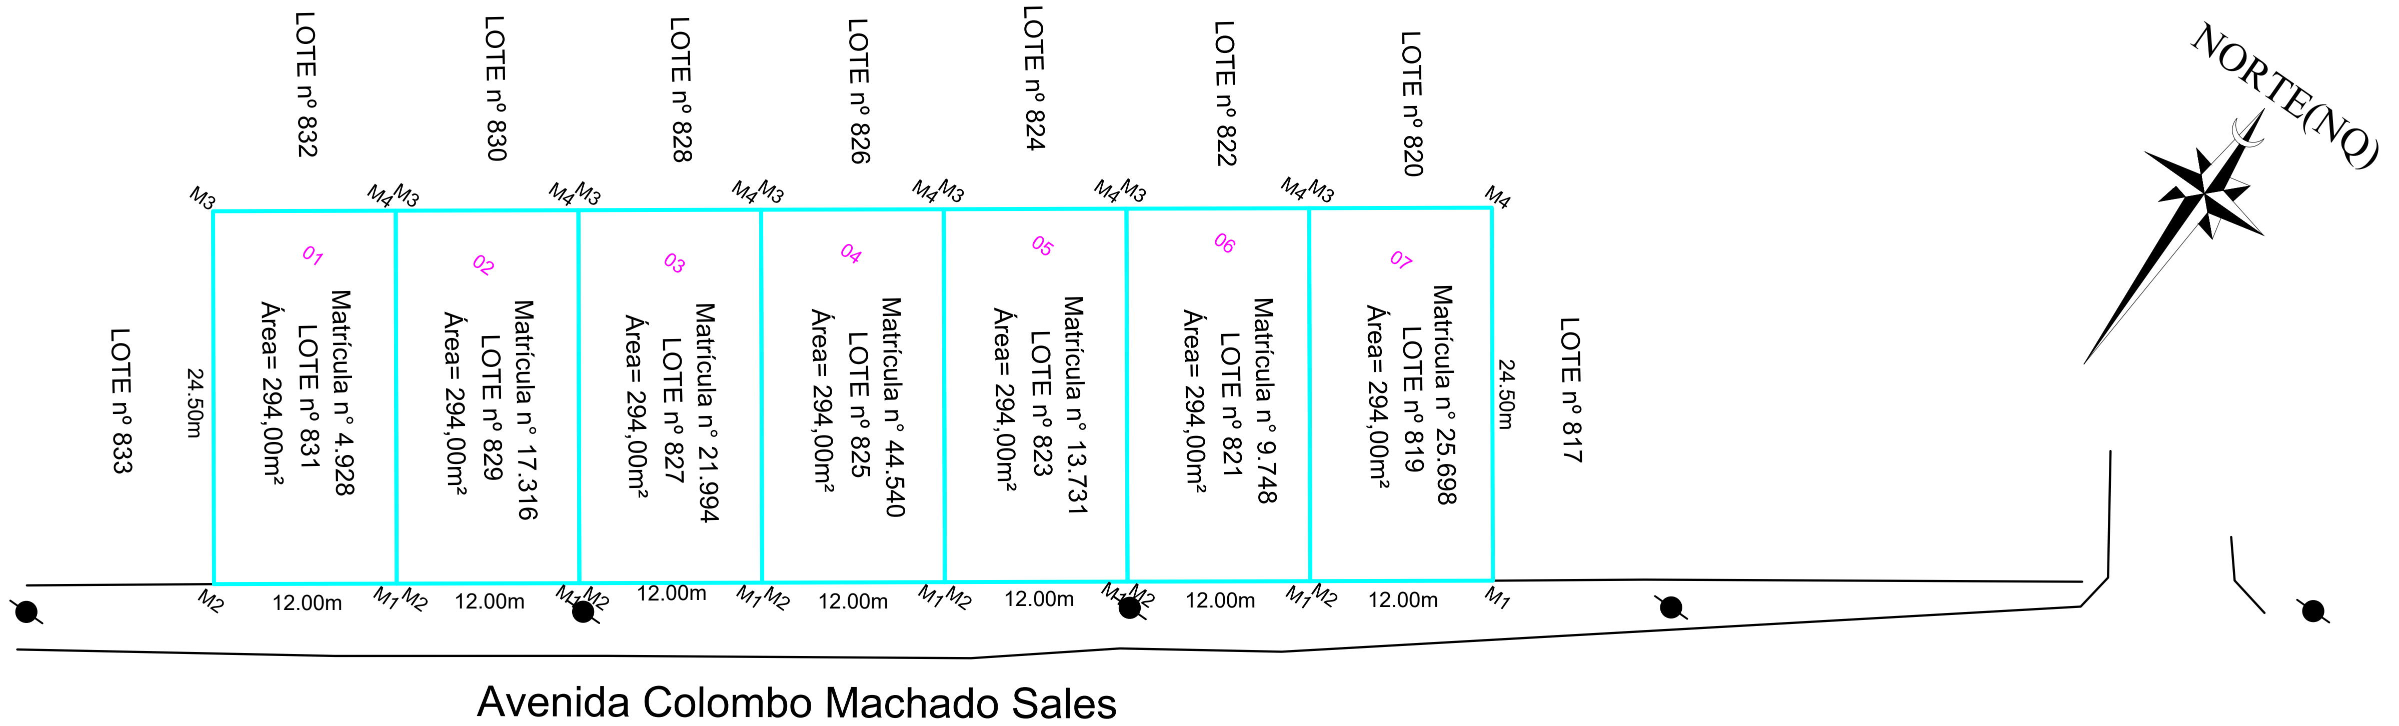
NORTE(NQ)
LOTE nº 832
LOTE nº 830
LOTE nº 828
LOTE nº 826
LOTE nº 824
LOTE nº 822
LOTE nº 820
LOTE nº 833
LOTE nº 817
01
02
03
04
05
06
07
Matrícula nº 4.928 LOTE nº 831 Área= 294,00m²
Matrícula nº 17.316 LOTE nº 829 Área= 294,00m²
Matrícula nº 21.994 LOTE nº 827 Área= 294,00m²
Matrícula nº 44.540 LOTE nº 825 Área= 294,00m²
Matrícula nº 13.731 LOTE nº 823 Área= 294,00m²
Matrícula nº 9.748 LOTE nº 821 Área= 294,00m²
Matrícula nº 25.698 LOTE nº 819 Área= 294,00m²
M1
M2
M3
M4
24.50m
12.00m
Avenida Colombo Machado Sales

SITUAÇÃO CONFORME AS MATRÍCULAS N° 4.928, N° 17.316, N° 21.994, N° 44.540, N° 13.731, N° 9.748 E N° 25.698

ESCALA 1/500

Projeção Universal Tranversa de Mercator (UTM) 22S
DATUM: SIRGAS 2000

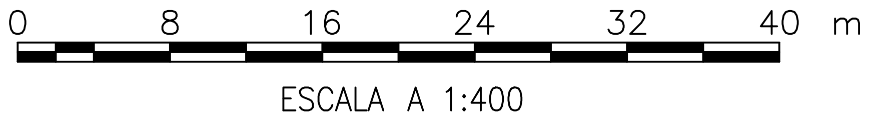

ESCALA A 1:400

JONAS TOPOGRAFIA
TOPOGRAFIA E AGRIMENSURA EM GERAL, USUCAPIÃO
WWW.JONASTOPOGRAFIA.COM.BR
jonasgesse@gmail.com
(48) 99934 7068 / 3733 4241

PROJETO: TOPOGRAFIA - UNIFICAÇÃO
DESCRIÇÃO: LEVANTAMENTO PLANIALTIMÉTRICO CADASTRAL
LOCAL: PEREQUÊ, PORTO BELO - SC

ENGENHEIRO E RESPONSÁVEL TÉCNICO
JONAS GESSE NUNES:00945941986
Assinado de forma digital por JONAS GESSE NUNES:00945941986
Dados: 2026.07.15 17:28:13 -03'00'
JONAS GESSÉ NUNES
CREA - SC : 116.343-3
CFT nº 009.459.419-86
G4N - registro do INCRA

PROPRIETÁRIO / REQUERENTE
ANDERSON CRISTIANO MAXIMIANO:00518628914
Assinado de forma digital por ANDERSON CRISTIANO MAXIMIANO:00518628914
Dados: 2026.07.15 18:48:49 -03'00'
MAXCES CONSTRUTORA
E INCORPORADORA LTDA
CNPJ n° 33.542.372/0001-07

ESCALA	ÁREAS	PERÍMETROS	DATA DO DESENHO	DATA DO LEVANTAMENTO	FOLHA
INDICADA	INDICADA	INDICADA	14/07/2026	04/09/2024	A2 01/001

DADOS
Levantamento planialtimétrico cadastral para fins de unificação um lote urbano da Matrícula n° 4.928 do Ofício do R.I. da Comarca de Tijucas, Matrícula n° 17.316 do Ofício do R.I de Porto Belo/SC (LOTE N° 829), Matrícula n° 21.994 do Ofício do R.I de Porto Belo/SC (LOTE N° 827), Matrícula n° 44.540 do Ofício do R.I de Porto Belo/SC (LOTE N° 825), Matrícula n° 13.731 do Ofício do R.I de Porto Belo/SC (LOTE N° 823), Matrícula n° 9.748 do Ofício do R.I de Porto Belo/SC (LOTE N° 821) e Matrícula n° 25.698 do R.I. de Tijucas (LOTE N° 819), com uma área total de 2.058,00m² localizado na Avenida Vereador Pedro Elias Rodrigues a 52,00 metros da Rua Moacir João Pedro, no bairro Perequê, Porto Belo/SC.