




PLANTA DE SITUAÇÃO
ESCALA: 1/1000

LEGENDA
- UNIDADES RESIDENCIAIS
- UNIDADES COMERCIAIS
- LAZER COBERTO
- LAZER DESCOBERTO
- LAZER ABERTO COBERTO
- CIRCULAÇÃO VERTICAL
- CIRCULAÇÃO HORIZONTAL
- ÁREA DE USO COMUM
- COBERTURA (SEM USO)
- RESERVATÓRIO
- RAMPA
- EMBASAMENTO
- PROJ.DA EDIF.
- ÁREA PERMEÁVEL
- ELEMENTO CONSTRUTIVO PROJETADO SOBRE O RECUO FRONTAL/AFASTAMENTOS
- CIRCULAÇÃO ELEVADA
- AREA ACESSO PÚBLICO

PLANTA PERÍMETRO - IMPLANTAÇÃO
ESCALA 1/100

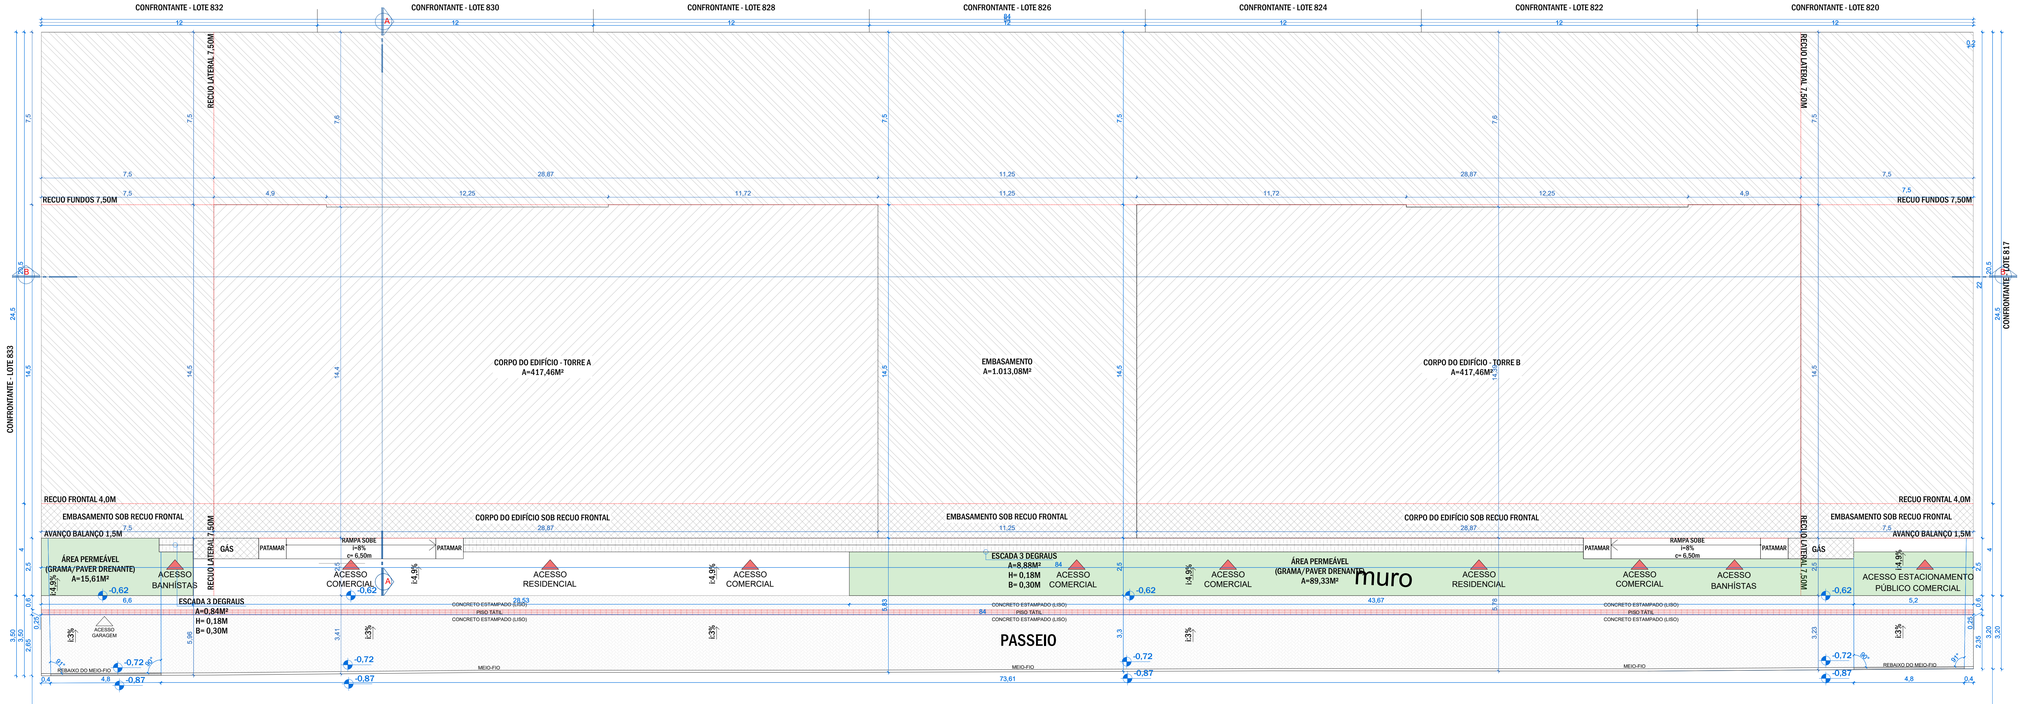

AVENIDA VEREADOR PEDRO ELIAS RODRIGUES

EIXO

PASSEIO

TERRENO - UNIFICAÇÃO DE LOTES
PROCESSO 9907/2025

Declaração de Responsabilidade

O(a) signatário(a) Sr(ª) **MAXCES CONSTRUTORA E INCORPORADORA** , legítima(a) proprietário(a) e/ ou possuidor(a) do imóvel aqui especificado, inscrito sob a inscrição imobiliária nº nº 01.01.060.0172; 01.01.060.0160; 01.01.060.0148; 01.01.060.0136; 01.01.060.0124; 01.01.060.0112; 01.01.060.0100. e a Sra Arq. JESSICA MUNHOZ VIEIRA, CAU nº A321019-7 responsável técnico pela elaboração deste Projeto, conforme ART/ RRT nº 16271179 declaram:

1.O(a) autor(a) do Projeto Legal reconhece que o presente projeto foi elaborado em estrita conformidade com as Normas Técnicas aplicáveis e com a legislação vigente nas esferas Municipal (Porto Belo), Estadual (Santa Catarina) e Federal, incluindo leis, decretos, normas técnicas de acessibilidade, normas de desempenho e demais dispositivos previstos no Plano Diretor do Município de Porto Belo.

2.O(as) signatário(as) declaram estar cientes de que, caso seja constatada qualquer execução de obra em desacordo com as Normas Técnicas ou com os dispositivos legais vigentes, o empreendimento estará sujeito às autuações e penalidades cabíveis pelos órgãos competentes, inclusive multas, bem como à não emissão do Habite-se por esta Secretaria até a devida regularização, sem prejuízo das demais sanções previstas em lei.

3. O(a) autor(a) do Projeto e o(a) proprietário(a) do imóvel são responsáveis, nas esferas civil, penal e administrativa, pelo fiel atendimento às especificações estabelecidas na legislação e no decreto vigente que dispõe sobre os procedimentos relativos à aprovação de projetos.

4. A aprovação dos projetos pela Prefeitura Municipal não implica, em nenhuma hipótese, no reconhecimento do direito de propriedade do imóvel.

5.Conforme as informações constantes na Consulta Prévia, é permitida pela divisão de normas urbanísticas, desmembrar de acordo com a legislação urbanística vigente do Município de Porto Belo, especialmente no que se refere ao recuo frontal, declaro que me responsabilizo pelo correto alinhamento predial no lote, estando ciente das penalidades previstas na legislação aplicável em caso de descumprimento.

6.Declaro que os projetos submetidos à aprovação junto aos demais órgãos competentes são compatíveis com aqueles apresentados à Secretaria de Planejamento Urbano.

7.Declaro, ainda, estar ciente do conteúdo, da obrigatoriedade e da necessidade de integral cumprimento das seguintes legislações e normas técnicas vigentes, bem como de suas alterações:

Legislação Federal
- Lei Federal nº 10.098/2000 - Normas gerais e critérios básicos para a promoção da acessibilidade das pessoas portadoras de deficiência ou com mobilidade reduzida.
  - Lei Federal nº 10.741/2003 - Estatuto da Pessoa Idosa.
- Lei Federal nº 13.146/2015 - Estatuto da Pessoa com Deficiência.
- Decreto Federal nº 5.296/2004 - Normas e critérios básicos de acessibilidade.
- Decreto Federal nº 9.296/2018 - Acessibilidade em edificações de hospedagem.
- Decreto Federal nº 9.451/2018 - Acessibilidade em edificações multifamiliares.

Legislação Municipal
- Lei Complementar nº 34/2011 e suas alterações - Institui o Código de Obras do Município de Porto Belo.
  - Lei Complementar nº 35/2011 e suas alterações - Dispõe sobre o Código de Posturas do município de Porto Belo.
  - Lei Complementar nº 92/2014 - Institui o Código Tributário do Município de Porto Belo.
- Lei Complementar nº 124/2019 - Institui o Cone de Sombreamento como instrumento de política urbanística do Município de Porto Belo.
- Lei Complementar nº 194/2022 - Estabelece as diretrizes quanto à delimitação das faixas marginais de cursos d'água em área urbana consolidada e disciplina a ocupação das Áreas de Preservação Permanente no Município de Porto Belo.
- Lei Complementar nº 212/2023 - Regulamenta o Instrumento de Indução ao Desenvolvimento Urbano, da Outorga Onerosa do Direito de Construir no Município de Porto Belo.
- Lei Complementar nº 275/2025 - Institui o Zoneamento e o Ordenamento Territorial do Município de Porto Belo, definindo diretrizes para o uso e ocupação do solo e os limites do planejamento urbano municipal.
  - Lei Complementar nº 276/2025 - Institui o Plano Diretor de Gestão e Desenvolvimento Territorial de Porto Belo/SC.
  - Lei Complementar nº 277/2025 - Institui as Normas de Uso e Ocupação do Solo do Município de Porto Belo/SC.
  - Lei Complementar nº 278/2025 - Dispõe sobre o Parcelamento do Solo Urbano no Município de Porto Belo/SC.
- Lei Ordinária nº 1.147/2000 - Dispõe sobre a Eliminação de Barreiras Arquitetônicas em Edificações e Logradouros de Uso Público.
  - Lei Ordinária nº 2.146/2014 - Institui e integra as taxas ao sistema tributário municipal de Porto Belo - SC.
- Lei Ordinária nº 2.859/2020 - Regulamenta o uso de equipamento bate estaca na construção civil no Município de Porto Belo.
  - Lei Ordinária nº 3.970/2025 - Estabelece diretrizes para a autorização e execução de obras e serviços de terraplenagem no Município de Porto Belo.
- Decreto nº 17/2003 - Cria métodos para as consultas de viabilidade e alvarás de construção em áreas alodiais e terrenos de marinha.
- Decreto nº 1.132/2013 - Estrutura o Programa de Preservação e Recuperação da Identidade Açoriana no que se refere a caracterização da arquitetura e regulamenta e dispositivos do Plano Diretor.
  - Decreto nº 1.243/2014 - Determina o padrão para pavimentação de calçadas e colocação de lixeiras.
- Resolução nº 01/2015 - Orienta e determina a análise de projetos com garagem descoberta ou coberta, bem como a edificação geminada e vaga de estacionamento.
- Resolução nº 01/2021 - Orienta e determina as condições gerais para construção e execução de rebaixos de meio-fio no Município de Porto Belo.

Normas Técnicas - ABNT
- NBR 8160:1999 - Sistemas prediais de esgotos sanitários - Projeto e execução.
- NBR 17076:2024 - Projeto de sistema de tratamento de esgoto de menor porte - Requisitos.
- NBR 9050:2020 - Acessibilidade a edificações, mobiliário, espaços e equipamentos urbanos.
- NBR 16537:2024 - Acessibilidade - Sinalização tátil no piso - Diretrizes para elaboração de projetos e instalação.
- NBR 15575-1:2025 - Edificações habitacionais - Desempenho Parte 1: Requisitos gerais.
- NBR 15575-2:2013 - Edificações habitacionais - Desempenho Parte 2: Requisitos para os sistemas estruturais.
- NBR 15575-3:2021 - Edificações habitacionais - Desempenho Parte 3: Requisitos para os sistemas de pisos.
- NBR 15575-4:2025 - Edificações habitacionais - Desempenho Parte 4: Requisitos para os sistemas de vedações verticais internas e externas - SVVIE.
- NBR 15575-5:2025 - Edificações habitacionais - Desempenho Parte 5: Requisitos para os sistemas de coberturas.
- NBR 15575-6:2021 - Edificações habitacionais - Desempenho Parte 6: Requisitos para os sistemas hidrossanitários.

8. As instalações hidrossanitárias internas à edificação, bem como a previsão e dimensionamento do reservatório de água potável, são de inteira responsabilidade do(a) responsável técnico(a) pelo projeto.

Porto Belo, 09 de setembro de 2026.

MAXCES CONSTRUTORA E INCORPORADORA LTDA
CNPJ 33.542.372/0001-07

Proprietário(a)
MAXCES CONSTRUTORA E INCORPORADORA LTDA

gov.br Documento assinado digitalmente
JESSICA MUNHOZ VIEIRA
Data: 10/09/2026 16:49:08-0300
Verifique em https://validar.iti.gov.br

Responsável(is) Técnico(s) dos Projetos
JÉSSICA MUNHOZ VIEIRA,
CAU nº A321019-7

ESTATISTICAS

INFORMAÇÕES DOS LOTES

INSCRIÇÃO IMOBILIÁRIA: 01.01.060.0172; 01.01.060.0160; 01.01.060.0148; 01.01.060.0136; 01.01.060.0124; 01.01.060.0112; 01.01.060.0100. e a Sra Arq. JESSICA MUNHOZ VIEIRA, CAU nº A321019-7 responsável técnico pela elaboração deste Projeto, conforme ART/ RRT nº 16271179 declaram:

ÁREA DO TERRENO	2058,00 m²
TESTADA DO LOTE	84,00 m
EMBASAMENTO	1013,08 m²
1º PAVIMENTO TÉRREO - TOTAL	**1722,00 m²**

	A. PÚBLICA	A. COMERCIAL	A. RESIDENCIAL
2º PAVIMENTO G1 (Garagem pública / comercial/ residencial)	925,46	92,13	830,41
2º PAVIMENTO G1 - TOTAL			**1848,00 m²**
3º PAVIMENTO G2 - TOTAL			**1848,00 m²**
4º PAVIMENTO G3 - TOTAL			**1848,00 m²**
5º PAVIMENTO G4 - TOTAL			**1848,00 m²**
6º PAVIMENTO G5 - TOTAL			**1848,00 m²**
7º PAVIMENTO G6 - TOTAL			**1848,00 m²**

	A. COBERTA	A. DESCOBERTA
8º PAVIMENTO LAZER	834,92	1013,08
8º PAVIMENTO LAZER - TOTAL		**1848,00 m²**

PAVIMENTO TIPO 01 (10 studios e 4 aptos com dois dormitórios)	834,92 m²
9º/10º/11º/12º/13º/14º/15º/16º/17º/18º/22º/23º/24º/25º/26º/27º/34º-PAVIMENTO - TIPO 01 X	**17 14.193,64 m²**
PAVIMENTO TIPO 02 (10 studios e 2 aptos com dois dormitórios)	875,47 m²
19ºPAVIMENTO - TIPO 02 X	**1 875,47 m²**
PAVIMENTO TIPO 03 (10 studios, 2 aptos com dois dormitórios)	694,34 m²
20º/21º PAVIMENTO - TIPO 03 X	**2 1.388,68 m²**
PAVIMENTO TIPO 04 (10 studios e 3 aptos com dois dormitórios)	834,92 m²
28º PAVIMENTO - TIPO 04 X	**1 834,92 m²**
PAVIMENTO TIPO 05 (10 studios, 3 aptos com dois dormitórios)	764,63 m²
29º PAVIMENTO - TIPO 05 X	**1 764,63 m²**
PAVIMENTO TIPO 06 (10 studios, 2 aptos com dois dormitórios)	764,63 m²
30ºPAVIMENTO - TIPO 06 X	**1 764,63 m²**
PAVIMENTO TIPO 07 (10 studios, 3 aptos com dois dormitórios)	764,63 m²
31º/32º PAVIMENTO - TIPO 07 X	**2 1.529,26 m²**
PAVIMENTO TIPO 08 (06 lofts studio, 06 lofts aptos com três dormitórios)	834,92 m²
33º PAVIMENTO - TIPO 08X	**1 834,92 m²**
MEZANINO PAVIMENTO TIPO 08	321,96 m²
MEZANINO 33º PAVIMENTO - TIPO 08 X	**1 321,96 m²**

	A. PASSARELA	A. COBERTA	A. DESCOBERTA
35º PAVIMENTO - LAZER ROOFTOP / PASSARELA	33,19	91,76	123,38
35º PAVIMENTO - APARTAMENTOS / CIRCULAÇÕES			**618,84 m²**
35º PAVIMENTO - TOTAL (Lazer / Rooftop + Tipo 09X01 / Circulações)			**867,17 m²**
BARRILETE, CASA DE BOMBAS, CAIXA D'ÁGUA			**276,38 m²**
ÁREA TOTAL CONSTRUIDA			**37.309,61 m²**

ÍNDICES URBANISTICOS	
ZONEAMENTO	**MUQ-5**
ÁREA MÁXIMA OCUPADA	**1848,00 m²**
TAXA DE OCUPAÇÃO	89,80%
COEFICIENTE DE APROVEITAMENTO UTILIZADO	18,13
GABARITO	118,10 m
EMBASAMENTO	22,80 m
ÁREA PERMEÁVEL	104,94 m²
TAXA DE PERMEABILIDADE	5,10%
NÚMERO DE DORMITÓRIOS	458
OUTORGA ONEROSA	
ÁREA COMPUTÁVEL (9º AO 35º PVTO)	22.375,23 m²
ÁREA PERMITIDA (2058,00m² x 1,25)	2.572,50 m²
ÁREA DE COBRANÇA DE OUTORGA	19.802,73 m²

QUADRO DE INFORMAÇÕES - APTOS/STUDIOS

APARTAMENTOS TORRE A	NUM. QUARTOS
APARTAMENTO 901-A À 3201-A/ 3401-A	2
STUDIO 902-A À 3202-A/ 3402-A	1
STUDIO 903-A À 3203-A/ 3403-A	1
STUDIO 904-A À 3204-A/ 3404-A	1
STUDIO 905-A À 3205-A/ 3405-A	1
STUDIO 906-A À 3206-A/ 3406-A	1
APARTAMENTO 907-A À 1807-A / 2207-A À 2707-A / 3207-A/ 3407-A	2
LOFT STUDIO 3301-A E 3305-A	3
LOFT APTO 3302-A	3
LOFT APTO 3303-A	1
LOFT APTO 3304-A	1
LOFT APTO 3306-A	1
APARTAMENTO 3501-A	4
APARTAMENTOS TORRE B	**NUM. QUARTOS**
APARTAMENTO 901-B À 1801-B / 2201-B À 2901-B/ 3401-B	2
STUDIO 902-B À 3202-B/ 3402-B	1
STUDIO 903-B À 3203-B/ 3403-B	1
STUDIO 904-B À 3204-B/ 3404-B	1
STUDIO 905-B À 3205-B/ 3405-B	1
STUDIO 906-B À 3206-B/ 3406-B	1
APARTAMENTO 907-B À 3207-B/ 3407-B	2
LOFT STUDIO 3301-A E 3305-B	3
LOFT APTO 3302-B	1
LOFT APTO 3303-B	1
LOFT APTO 3304-B	1
LOFT APTO 3306-B	1
APARTAMENTO 3501-B	4

QUADRO DE INFORMAÇÕES - ÁREA COMUM	
LAZER - 7º PVTO	02 BWC PNE
LAZER - 35º PVTO	02 BWC PNE

VAGAS DE ESTACIONAMENTO

COBERTAS PADRÃO	08 SIMPLES COM. + 291 SIMPLES RESID. = 299	363
TRIPLAS = 12 DUPLAS = 52		
DESCOBERTAS PADRÃO		0
PCD EXTRAS COBERTAS		7
TOTAL COMERCIAL		8
TOTAL RESIDENCIAL		262
TOTAL		**370**

QUADRO DE INFORMAÇÕES - APTOS/STUDIO

APARTAMENTOS TORRE A	ÁREA
APARTAMENTO 901-A À 3201-A/ 3401-A	73,40 m²
STUDIO 902-A À 3202-A/ 3402-A	38,00 m²
STUDIO 903-A À 3203-A/ 3403-A	37,28 m²
STUDIO 904-A À 3204-A/ 3404-A	37,28 m²
STUDIO 905-A À 3205-A/ 3405-A	38,00 m²
STUDIO 906-A À 3206-A/ 3406-A	36,51 m²
APARTAMENTO 907-A À 1807-A / 2207-A À 2707-A / 3207-A/ 3407-A	73,40 m²
LOFT STUDIO 3301-A E 3305-A	108,46 m²
LOFT APTO 3302-A	111,43 m²
LOFT APTO 3303-A	55,67 m²
LOFT APTO 3304-A	56,50 m²
LOFT APTO 3306-A	54,31 m²
APARTAMENTO 3501-A	231,12 m²
TOTAL DE UNIDADES TORRE A	**176**
APARTAMENTOS TORRE B	ÁREA
APARTAMENTO 901-B À 1801-B / 2201-B À 2901-B/ 3401-B	73,40 m²
STUDIO 902-B À 3202-B/ 3402-B	38,00 m²
STUDIO 903-B À 3203-B/ 3403-B	37,28 m²
STUDIO 904-B À 3204-B/ 3404-B	37,28 m²
STUDIO 905-B À 3205-B/ 3405-B	38,00 m²
STUDIO 906-B À 3206-B/ 3406-B	36,51 m²
APARTAMENTO 907-A À 3207-B/ 3407-B	73,40 m²
LOFT STUDIO 3301-A E 3305-B	108,46 m²
LOFT APTO 3302-B	56,50 m²
LOFT APTO 3303-B	55,67 m²
LOFT APTO 3304-B	111,43 m²
LOFT APTO 3306-B	54,31 m²
APARTAMENTO 3501-B	231,12 m²
TOTAL DE UNIDADES TORRE B	**176**
TOTAL DE UNIDADES TORRE A+B	**352**

QUADRO DE INFORMAÇÕES - SALAS COMERCIAIS

SALA COMERCIAL 01	62,82 m²
SALA COMERCIAL 02	143,26 m²
SALA COMERCIAL 03	764,63 m²
SALA COMERCIAL 04	104,48 m²
SALA COMERCIAL 05	114,07 m²
SALA COMERCIAL 06	104,74 m²
SALA COMERCIAL 07	53,87 m²
TOTAL DE UNIDADES	**7**

QUADRO DE INFORMAÇÕES - VAGAS COMERCIAIS/PÚBLICAS


NÚMERO DA VAGA	ÁREA TOTAL
VAGA PCD COMERCIAL 07/ 08	12,50 m²
VAGA COMERCIAL 01/ 06	10,80 m²
VAGA COMERCIAL 02/ 03	11,23 m²
VAGA COMERCIAL 04/ 05	11,10 m²
VAGA PÚBLICA 01	11,01 m²
VAGA PÚBLICA 02	11,34 m²
VAGA PÚBLICA 03	11,13 m²
VAGA PÚBLICA 04/ 05	11,21 m²
VAGA PÚBLICA 06/ 11/ 14/ 24/ 28	10,80 m²
VAGA PÚBLICA 07/ 08	11,50 m²
VAGA PÚBLICA 09/ 10/ 12/ 13	11,10 m²
VAGA PÚBLICA 15	11,23 m²
VAGA PÚBLICA 16	11,37 m²
VAGA PÚBLICA 17	10,94 m²
VAGA PÚBLICA 18	10,98 m²
VAGA PÚBLICA 19/ 20	12,43 m²
VAGA PÚBLICA 21/ 22/ 23	12,00 m²
VAGA PÚBLICA 25	13,00 m²
VAGA PÚBLICA 26 / 27	11,30 m²
TOTAL DE UNIDADES	**36**

QUADRO DE INFORMAÇÕES - VAGAS RESIDENCIAIS

VAGA EXTRA PCD (USO COMUM DO CONDOMÍNIO) - 01/ 02/ 03/ 04/ 05/ 06/07	10,80 m²
VAGA SIMPLES 01/ 02/ 03/ 23/ 24/ 25/ 63/ 64/ 65/ 77/ 78/ 79/ 115/ 116/ 117/ 132/ 133/ 171/ 172/ 173/ 185/ 186/ 187/ 225/ 226/ 227/ 239/ 240/ 241/ 279/ 280/ 281	11,52 m²
VAGA SIMPLES 04/ 05/ 26/ 27/61/ 62/ 80/ 81/ 115/ 116/ 134/ 135/ 169/ 170/ 188/ 189/ 223/ 224/ 242/ 243/ 277/ 278	12,43 m²
VAGA SIMPLES 06/ 28/ 60/ 82/ 114/ 136/ 168/ 190/ 222/ 244/ 276	10,98 m²
VAGA SIMPLES 07/ 29/ 83/ 135/ 191/ 245	10,87 m²
VAGA SIMPLES 08/ 30/ 84/ 138/ 192/ 246	11,28 m²
VAGA SIMPLES 09/ 31/ 85/ 139/ 193/ 247	11,27 m²
VAGA SIMPLES 10 / 13/ 16/ 32/ 33/ 35/ 38/ 45/ 50/ 53/ 56/ 76/86/ 89/ 92/ 99/ 104/ 107/ 110/ 130/ 140/ 143/ 146/ 153/ 158/ 161/ 164/ 184/ 194/ 197/ 200/ 207/ 212/ 213/ 218/ 230/ 248/ 251/ 254/ 261/ 266/ 269/ 272/ 291	10,80 m²
VAGA SIMPLES 11/ 12/ 14/ 15/ 17/ 18/ 33/ 34/ 36/ 37/ 39/ 40/ 48/ 49/ 51/ 52/ 54/ 55/ 87/ 88/ 90/ 91/ 93/ 94/ 102/ 103/ 105/ 106/ 108/ 109/ 141/ 142/ 144/ 145/ 147/ 148/ 156/ 157/ 159/ 160/ 162/ 163/ 195/ 196/ 198/ 199/ 201/ 202/ 210/ 211/ 213/ 214/ 216/ 217/ 249/ 250/ 252/ 253/ 255/ 256/ 264/ 265/ 267/ 268/ 270/ 271/	11,10 m²
VAGA SIMPLES 19/ 72/ 126/ 180/ 234	11,17 m²
VAGA SIMPLES 20	36,87 m²
VAGA SIMPLES 21/ 66/ 75/ 120/ 129/ 174/ 183/ 228/ 237/ 282/ 290	13,00 m²
VAGA SIMPLES 41/ 46/ 47/ 57/ 95/ 100/ 101/ 111/ 149/ 154/ 155/ 169/ 203/ 208/ 209/ 215/ 257/ 262/ 263/ 273	11,23 m²
VAGA SIMPLES 42/ 96/ 150/ 204/ 258	11,24 m²
VAGA SIMPLES 43/ 44/ 97/ 98/ 151/ 152/ 205/ 206/ 259/ 260	11,50 m²
VAGA SIMPLES 58/ 112/ 166/ 220/ 274	11,37 m²
VAGA SIMPLES 59/ 113/ 167/ 221/ 275	10,94 m²
VAGA SIMPLES 67/ 68/ 121/ 122/ 175/ 176/ 229/ 230/ 283	16,37 m²
VAGA SIMPLES 69/ 70 / 123/ 124/ 177/ 178/ 231/ 232/ 284/285	11,31 m²
VAGA SIMPLES 71/ 125/ 179/ 233/ 286	12,32 m²
VAGA SIMPLES 73/ 127/ 181/ 235/ 287/288	11,34 m²
VAGA SIMPLES 74/ 128/ 182/ 236/ 289	11,06 m²
VAGA DUPLA 01	23,34 m²
VAGA DUPLA 02	23,79 m²
VAGA DUPLA 03	23,01 m²
VAGA DUPLA 04/ 13/ 22/ 31/ 40/ 52	21,60 m²
VAGA DUPLA 05/ 14/ 23/ 32	31,13 m²
VAGA DUPLA 06/ 15/ 24/ 33	31,59 m²
VAGA DUPLA 07/ 16/ 25/ 34	30,75 m²
VAGA DUPLA 08/ 17/ 26/ 35/ 47	22,60 m²
VAGA DUPLA 09/ 18/ 27/ 36/ 48	22,61 m²
VAGA DUPLA 10/ 19/ 28/ 37/ 49	22,30 m²
VAGA DUPLA 11/ 20/ 29/ 38/ 50	22,64 m²
VAGA DUPLA 12/ 21/ 30/ 39/ 51	21,94 m²
VAGA DUPLA 41/ 42/ 43	22,05 m²
VAGA DUPLA 44	27,78 m²
VAGA DUPLA 45	28,20 m²
VAGA DUPLA 46	27,46 m²
VAGA TRIPLA 01/ 02/ 04/ 05/07 / 08/ 10/ 11	33,21 m²
VAGA TRIPLA 03/ 06/ 09/ 12	33,18 m²
TOTAL DE UNIDADES	**362**

PAVER DRENANTE
Dimensões da peça: 20x10x6
Peso/pc: 2,3Kg
Pçs/m²: 50
Vantagens do piso drenante em concreto poroso:
-Elimina superfícies inundadas
-Aumenta a infiltração de água do solo
-Melhora prática de manejamento da água da chuva

DETALHE PAVER DRENANTE
SEM ESCALA

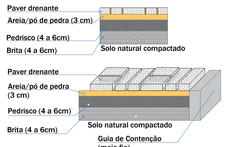

CARIMBOS PREFEITURA

Assinado digitalmente por: LUIS ANDRÉ RIOS 098.275.269-52
Data: 05/10/2026 13:22:46 -03'00'
Assinado digitalmente

ENGENHARIA - ARQUITETURA
CONSULTORIA TÉCNICA
RUA ANTÔNIO ZEFERINO STEIN - Nº 97
PEREQUÊ , PORTO BELO - SC/ CEP 88210-000, TEL: (47) 99923-3201
mvprojetosportobelo@gmail.com

PROJETO ARQUITETÔNICO
PORTO BELO FÁCIL

RESPONSÁVEL TÉCNICO:
gov.br Documento assinado digitalmente
JESSICA MUNHOZ VIEIRA
Data: 10/09/2026 16:53:47-0300
Verifique em https://validar.iti.gov.br

ARQ° JESSICA MUNHOZ VIEIRA
CAU-SC A321019-7

PROPRIETÁRIO:
MAXCES CONSTRUTORA E INCORPORADORA LTDA:33542372000107
Assinado de forma digital por MAXCES CONSTRUTORA E INCORPORADORA LTDA:33542372000107
Dados: 2026.09.10 14:31:05 -03'00'

MAXCES CONSTRUTORA E INCORPORADORA LTDA
CNPJ: 33.542.372/0001-07

DENOMINAÇÃO:
EDIFICAÇÃO RESIDENCIAL MULTIFAMILIAR E COMERCIAL
CONECTA TOWERS


ENDEREÇO:
AVENIDA VEREADOR PEDRO ELIAS RODRIGUES, n° 1600, LOTEAMENTO JARDIM DOURADO, BAIRRO ALTO PEREQUE - PORTO BELO - SC

CONTEÚDO:
PLANTA DE SITUAÇÃO
PLANTA PERÍMETRO - IMPLANTAÇÃO
QUADRO DE ÁREAS /DECLARAÇÃO /DETALHES

FOLHA
01/11


ESCALA:	DATA:	DESENHO TÉCNICO:	REVISÃO:
INDICADA	SET/2026	JESSICA MUNHOZ VIEIRA	02

ESTE DOCUMENTO É CÓPIA DO ORIGINAL ASSINADO DIGITALMENTE por LUIS ANDRE RIOS:09827526952 em 10/09/2026 13:22:46 -03'00' Para verificar as assinaturas vá ao site https://verificador.iti.br

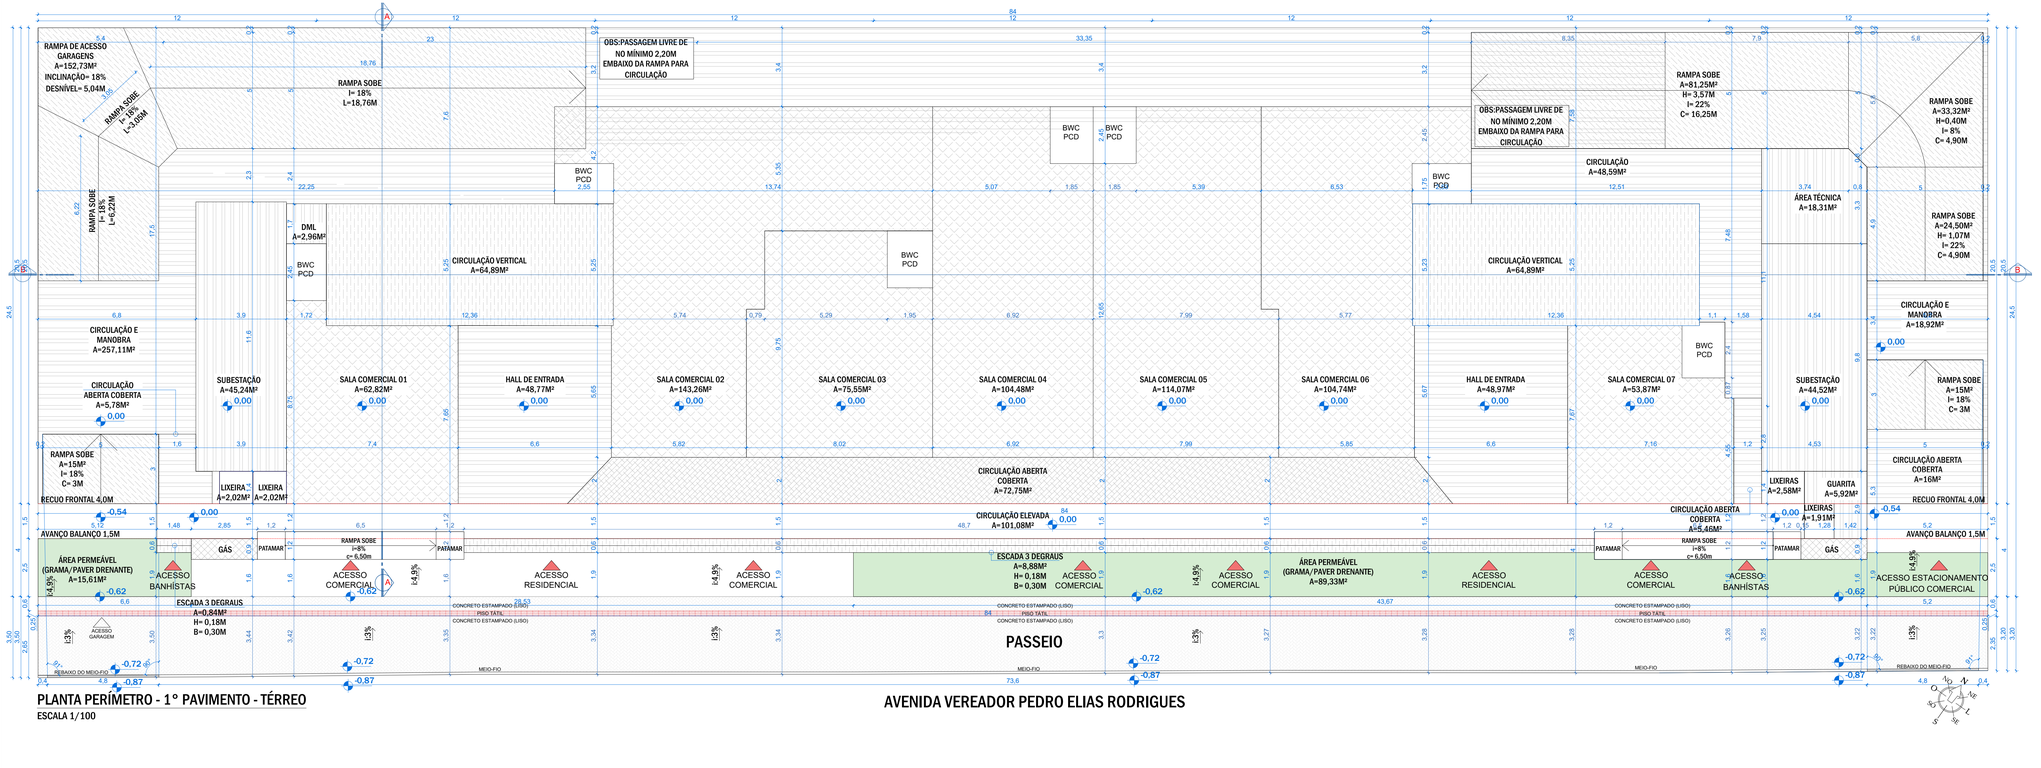

PLANTA PERÍMETRO - 1° PAVIMENTO - TÉRREO

ESCALA 1/100

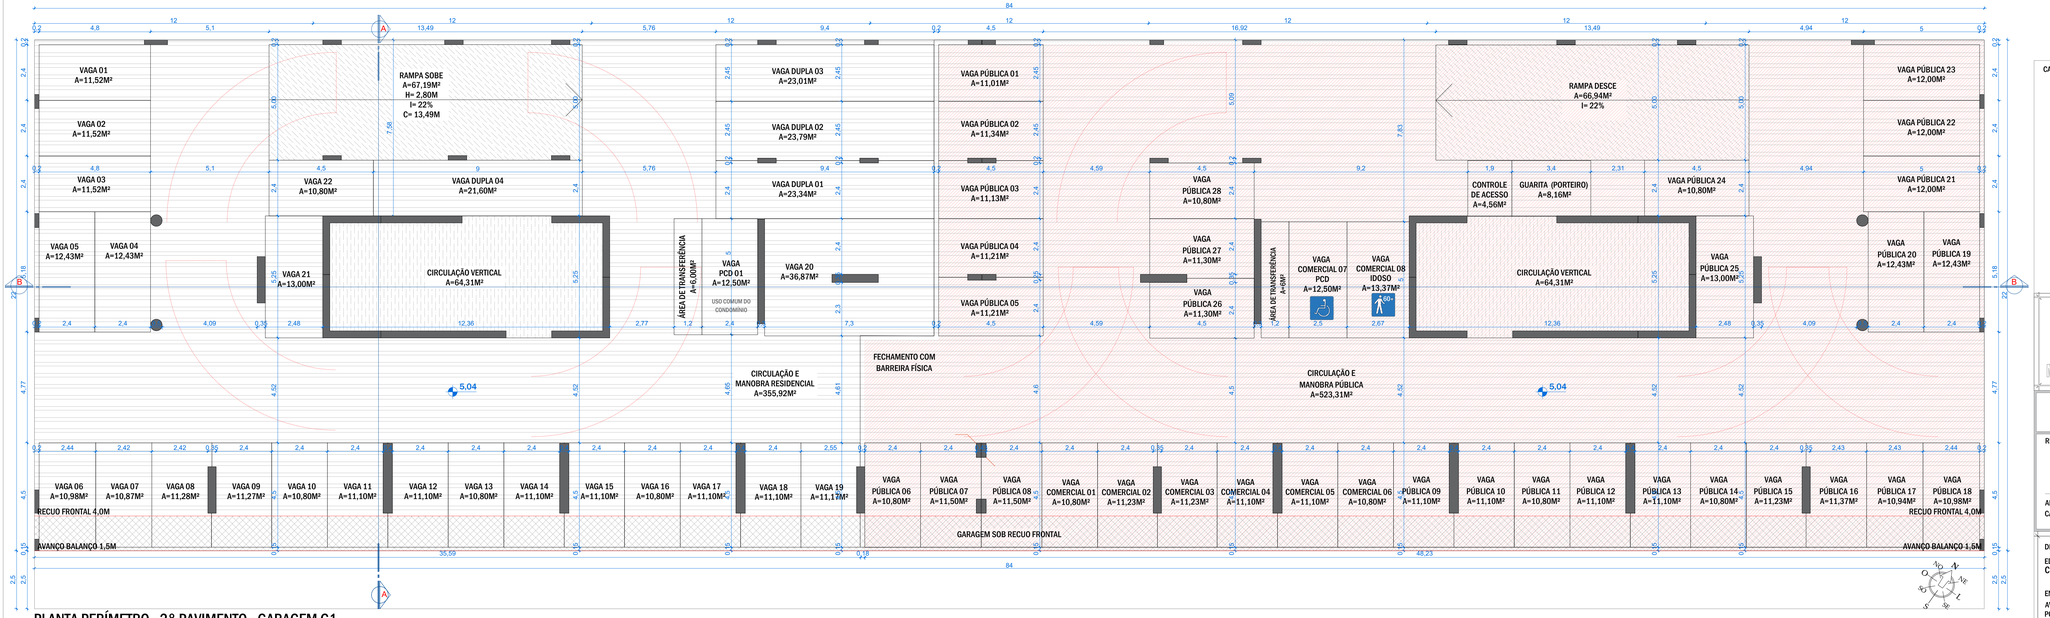

PLANTA PERÍMETRO - 2° PAVIMENTO - GARAGEM G1

ESCALA 1/100

NOTA: AREA INTERNA DE ACESSO PÚBLICO:

AREA TOTAL EM PLANTA A=1017,59M²

SENDO:

-AREA VAGAS PÚBLICAS: = 925,46M² (MÍNIMO 924,00M², EQUIVALENTE À 50% DO PAVIMENTO)

-AREA VAGAS COMERCIAIS = 92,13M² (06 VAGAS SIMPLES PADRÃO + 01 VAGA PCD + 01 VAGA IDOSO)

O CONTROLE DE ACESSO À CIRCULAÇÃO VERTICAL (ELEVADOR) ADOTARÁ CATRACA OU DISPOSITIVO SEMELHANTE DE CONTROLE.

PARA OS ELEVADORES SOCIAIS, SERÁ ADOTADO SISTEMA COM RESTRIÇÕES NO USO DO EQUIPAMENTO, GARANTINDO QUE APENAS PESSOAS AUTORIZADAS CHEGUEM AOS PAVIMENTOS RESIDENCIAIS.

QUANDO AO ACESSO À ESCADA DE EMERGÊNCIA, SERÁ PERMITIDO PELO PORTEIRO APENAS EM SITUAÇÕES DE EMERGÊNCIA NO EDIFÍCIO

LEGENDA

- UNIDADES RESIDENCIAIS
- UNIDADES COMERCIAIS
- LAZER COBERTO
- LAZER DESCOBERTO
- LAZER ABERTO COBERTO
- CIRCULAÇÃO VERTICAL
- CIRCULAÇÃO HORIZONTAL
- ÁREA DE USO COMUM
- COBERTURA (SEM USO)
- RESERVATÓRIO
- RAMPA
- EMBASAMENTO
- PROJ.DA EDIF.
- ÁREA PERMEÁVEL
- ELEMENTO CONSTRUTIVO PROJETADO SOBRE O RECUO FRONTAL/AFASTAMENTOS
- CIRCULAÇÃO ELEVADA
- AREA ACESSO PÚBLICO

CARIMBOS PREFEITURA

Assinado digitalmente por: LUIS ANDRE DIOS 095.075.269-52 Assinado digitalmente 05/10/2026 13:22:59

ENGENHARIA - ARQUITETURA
CONSULTORIA TÉCNICA
RUA ANTÔNIO ZEFERINO STEIN - Nº 97
PEREQUÊ , PORTO BELO - SC/ CEP 88210-000. TEL: (47) 99923-3201
mvprojetosportobelo@gmail.com

PROJETO ARQUITETÔNICO

PORTO BELO FÁCIL

RESPONSÁVEL TÉCNICO:

Documento assinado digitalmente govbr JESSICA MUNHOZ VIEIRA Data: 30/09/2026 16:49:08-0300 Verifique em https://validar.iti.gov.br

ARQ° JESSICA MUNHOZ VIEIRA
CAU-SC A321019-7

PROPRIETÁRIO:

MAXCES CONSTRUTORA E INCORPORADORA LTDA:33543272000107 Assinado de forma digital por MAXCES CONSTRUTORA E INCORPORADORA LTDA:33543272000107 Dados: 2026.09.10 13:00:04 -03'00'

MAXCES CONSTRUTORA E INCORPORADORA LTDA
CNPJ: 33.542.372/0001-07

DENOMINAÇÃO:

EDIFICAÇÃO RESIDENCIAL MULTIFAMILIAR E COMERCIAL
CONECTA TOWERS

ENDEREÇO:

AVENIDA VEREADOR PEDRO ELIAS RODRIGUES, n°1600, LOTEAMENTO JARDIM DOURADO, BAIRRO ALTO PEREQUE - PORTO BELO - SC


CONTEÚDO:

PLANTA PERÍMETRO - 1° PAVIMENTO - TÉRREO
PLANTA PERÍMETRO - 2° PAVIMENTO - GARAGEM G1

FOLHA 02/11


ESCALA:	DATA:	DESENHO TÉCNICO:	REVISÃO:
INDICADA	SET/2026	JESSICA MUNHOZ VIEIRA	02

ESTE DOCUMENTO FOI ASSINADO DIGITALMENTE POR LUIS ANDRE DIOS:09507526952 EM: 05/10/2026 13:22:59 -03:00 PARA VERIFICAR AS ASSINATURAS VÁ AO SITE HTTPS://VALIDAR.ITI.GOV.BR E UTILIZE O CÓDIGO: 2a2d3ab2a0a0ab2a7e74

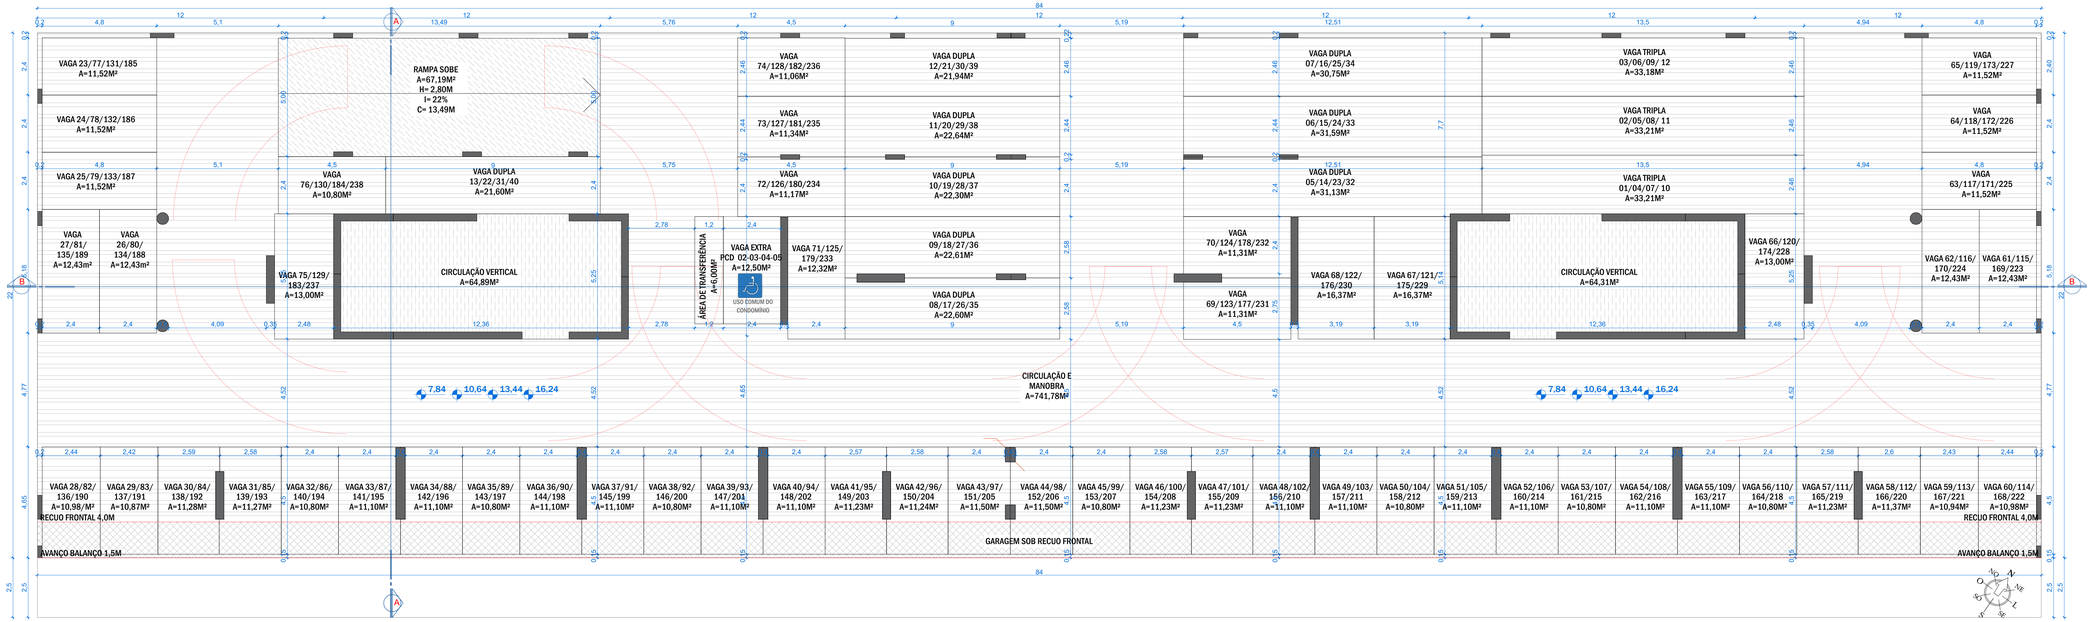

PLANTA PERÍMETRO - 3°/4°/5°/6° PAVIMENTO - GARAGEM G2/G3/G4/G5

ESCALA 1/100

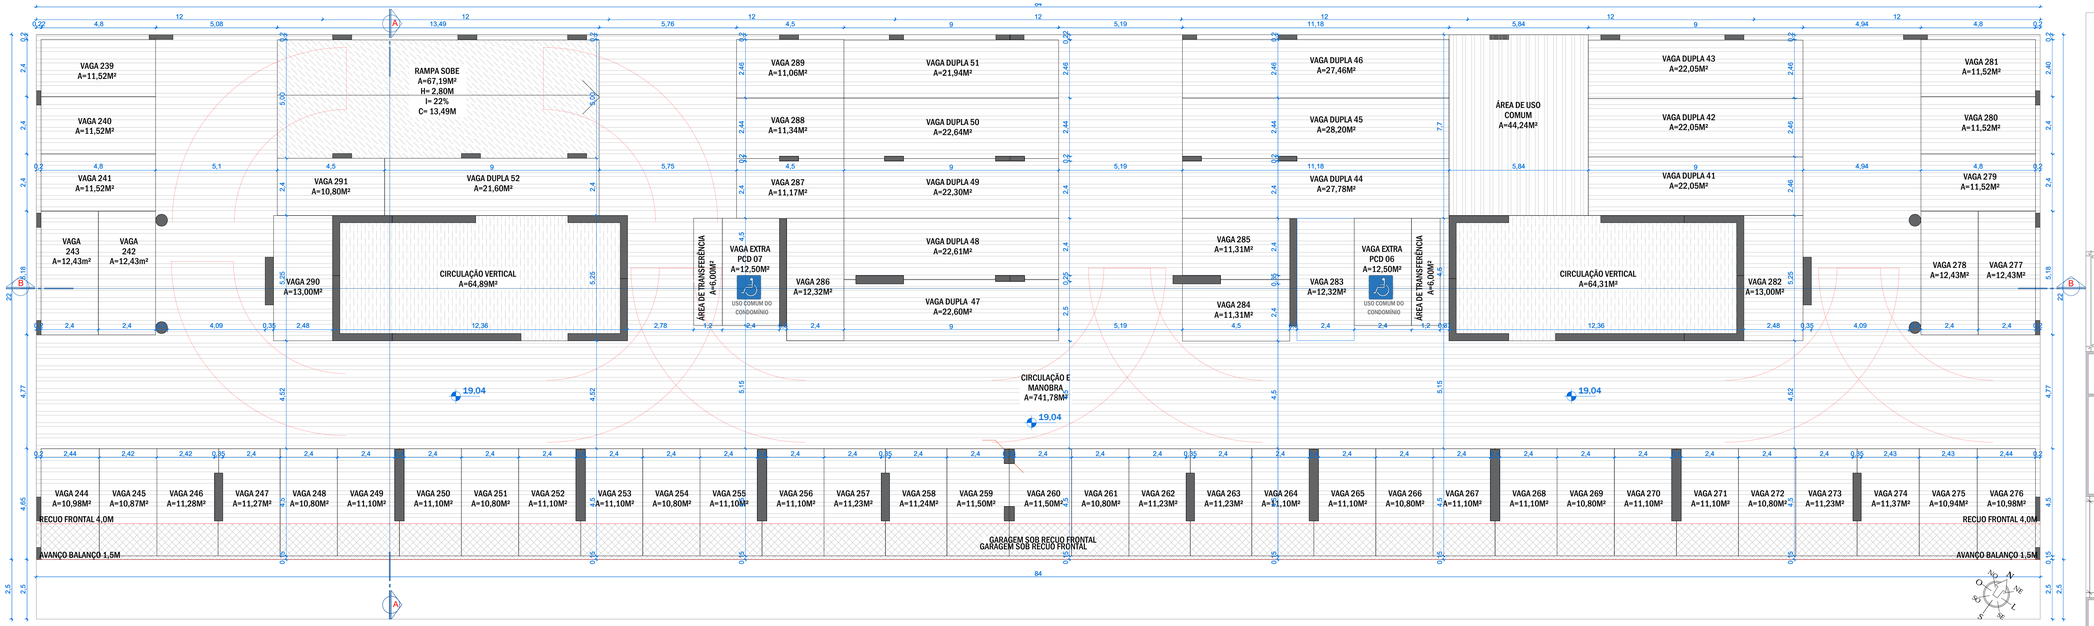

PLANTA PERÍMETRO - 7° PAVIMENTO - GARAGEM G6

ESCALA 1/100

LEGENDA

- UNIDADES RESIDENCIAIS
- UNIDADES COMERCIAIS
- LAZER COBERTO
- LAZER DESCOBERTO
- LAZER ABERTO COBERTO
- CIRCULAÇÃO VERTICAL
- CIRCULAÇÃO HORIZONTAL
- ÁREA DE USO COMUM
- COBERTURA (SEM USO)
- RESERVATÓRIO
- RAMPA
- EMBASAMENTO
- PROJ.DA EDIF.
- ÁREA PERMEÁVEL
- ELEMENTO CONSTRUTIVO PROJETADO SOBRE O RECUO FRONTAL/AFASTAMENTOS
- CIRCULAÇÃO ELEVADA
- AREA ACESSO PÚBLICO

CARIMBOS PREFEITURA

Assinado digitalmente por: LUIS ANDRÉ RIOS 098.375.269-52 05/10/2026 13:23:11

ESTE DOCUMENTO FOI ASSINADO DIGITALMENTE POR LUIS ANDRÉ RIOS:09837526952 E POR GOVBR:12345237200107 EM 05/10/2026 13:23:11 -03:00 VERIFIQUE EM HTTPS://VALIDAR.IO.GOV.BR/ COM O CÓDIGO: 1A2A.4C3A.6E5A.0B7D

MV PROJETOS
ENGENHARIA - ARQUITETURA
CONSULTORIA TÉCNICA
RUA ANTÔNIO ZEFERINO STEIN - Nº 97
PEREQUÊ , PORTO BELO - SC/ CEP 88210-000, TEL: (47) 99923-3201
mvprojetosportobelo@gmail.com

PROJETO ARQUITETÔNICO

PORTO BELO FÁCIL

RESPONSÁVEL TÉCNICO:

govbr Documento assinado digitalmente JESSICA MUNHOZ VIEIRA Data: 01/05/2026 16:49:06 -0300 Verifique em https://validar.iti.gov.br

ARQ° JESSICA MUNHOZ VIEIRA
CAU-SC A321019-7

PROPRIETÁRIO:

MAXCES CONSTRUTORA E INCORPORADORA LTDA:33542372000107 Assinado de forma digital por MAXCES CONSTRUTORA E INCORPORADORA LTDA:33542372000107 Dados: 2026.09.10 14:34:04 -03'00'

MAXCES CONSTRUTORA E INCORPORADORA LTDA
CNPJ: 33.542.372/0001-07

DENOMINAÇÃO:

EDIFICAÇÃO RESIDENCIAL MULTIFAMILIAR E COMERCIAL
CONECTA TOWERS

ENDEREÇO:


AVENIDA VEREADOR PEDRO ELIAS RODRIGUES, n°1600, LOTEAMENTO JARDIM DOURADO, BAIRRO ALTO PEREQUE - PORTO BELO - SC

CONTEÚDO:

PLANTA PERÍMETRO - 3°/4°/5°/6°/7° PAVIMENTO - GARAGEM G2/G3/G4/G5/G6

FOLHA 03/11


ESCALA:	DATA:	DESENHO TÉCNICO:	REVISÃO:
INDICADA	SET/2026	JESSICA MUNHOZ VIEIRA	02

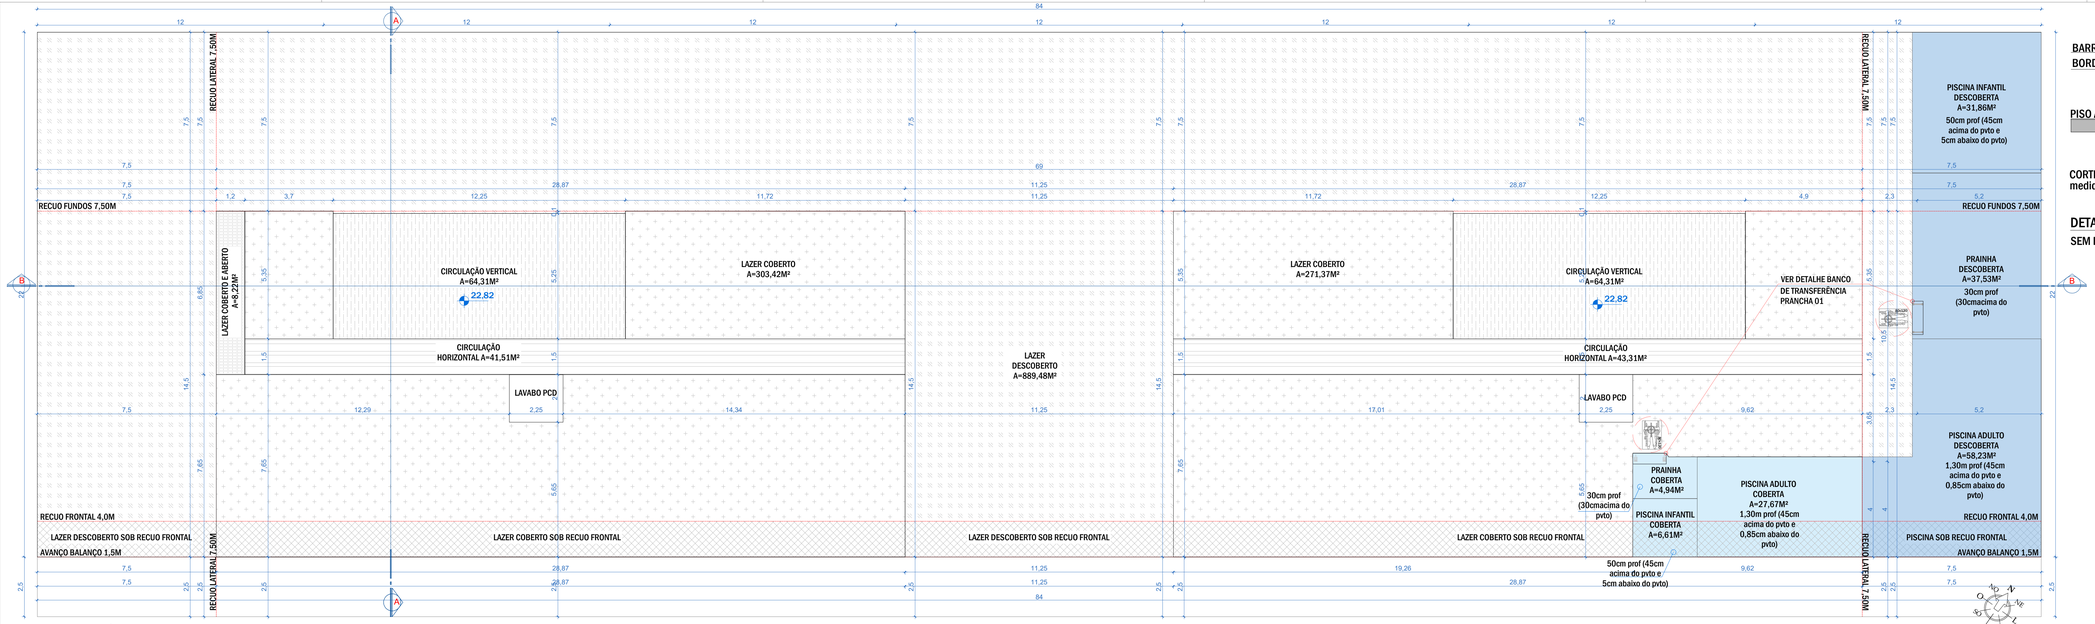

PLANTA PERÍMETRO - 8° PAVIMENTO - LAZER

ESCALA 1/100

CORTE ESQUEMÁTICO
medidas em cm

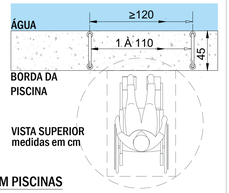


VISTA SUPERIOR
medidas em cm

DETALHE BANCO DE TRANSFERÊNCIA EM PISCINAS

SEM ESCALA

LEGENDA

- UNIDADES RESIDENCIAIS
- UNIDADES COMERCIAIS
- LAZER COBERTO
- LAZER DESCOBERTO
- LAZER ABERTO COBERTO
- CIRCULAÇÃO VERTICAL
- CIRCULAÇÃO HORIZONTAL
- ÁREA DE USO COMUM
- COBERTURA (SEM USO)
- RESERVATÓRIO
- RAMPA
- EMBASAMENTO
- PROJ.DA EDIF.
- ÁREA PERMEÁVEL
- ELEMENTO CONSTRUTIVO PROJETADO SOBRE O RECUO FRONTAL/AFASTAMENTOS
- CIRCULAÇÃO ELEVADA
- AREA ACESSO PÚBLICO

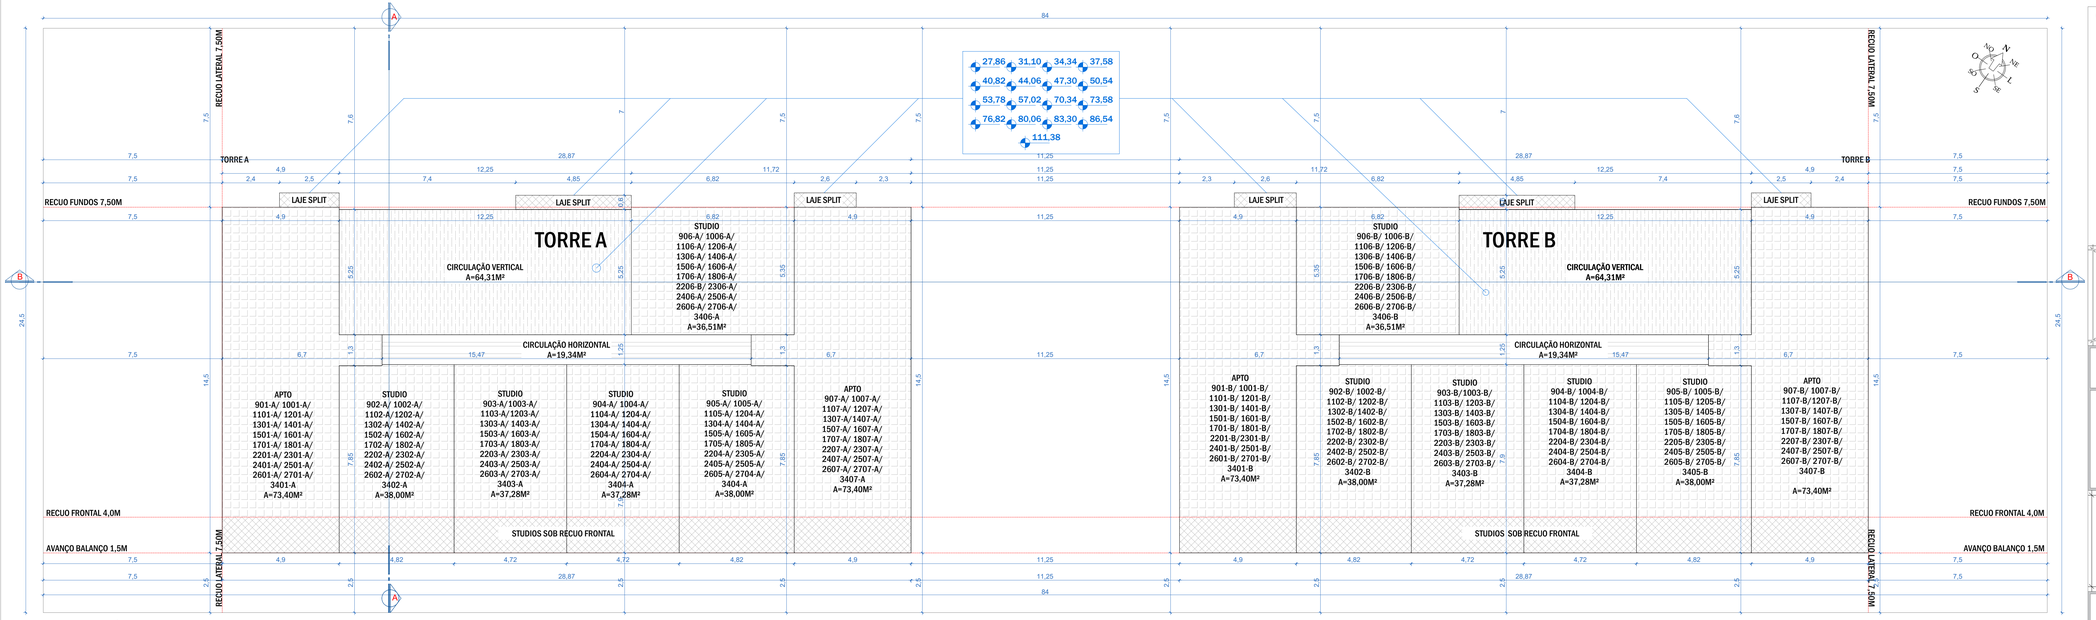


PLANTA PERÍMETRO - 9°/10°/11°/12°/13°/14°/15°/16°/17°/18°/22°/23°/24°/25°/26°/27°/34° PAVIMENTO - TIPO 01 X17

ESCALA 1/100

CARIMBOS PREFEITURA


Assinado digitalmente por: LUIS ANDRÉ RIOS 098.275.269-62 assinado 05/10/2026 13:23:22

ESTE DOCUMENTO FOI ASSINADO DIGITALMENTE POR LUIS ANDRÉ RIOS EM 05/10/2026 13:23:22 GMT-03:00
VERIFIQUE A AUTENTICIDADE DO DOCUMENTO EM HTTPS://VALIDAR.ITI.GOV.BR COM O CÓDIGO 2.16.76.1.12.1.2.0.0.0

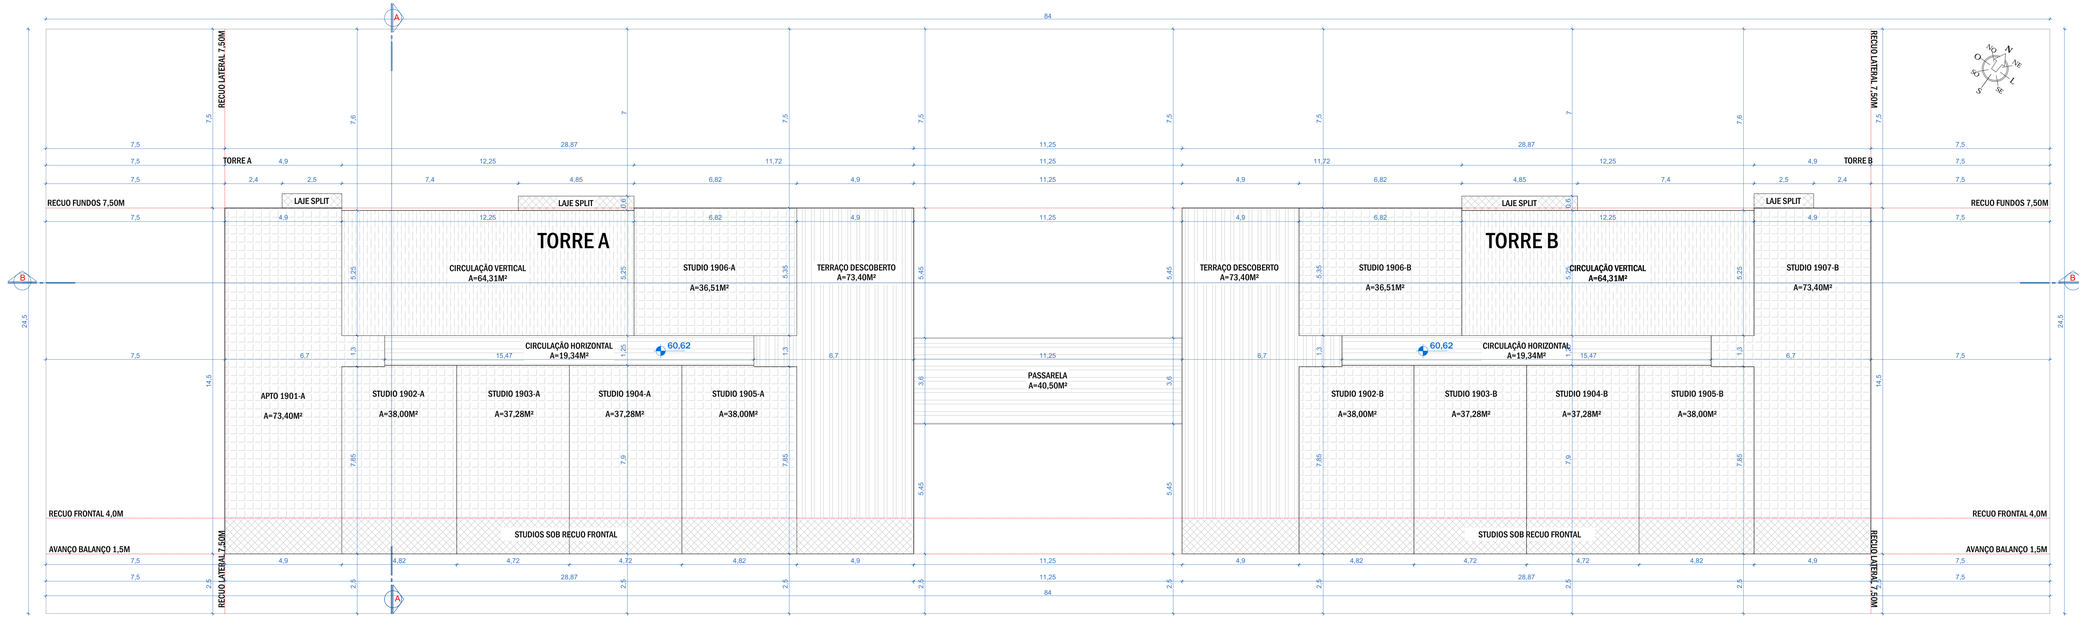

PLANTA PERÍMETRO - 19° PAVIMENTO - TIPO 02 X01

ESCALA 1/100

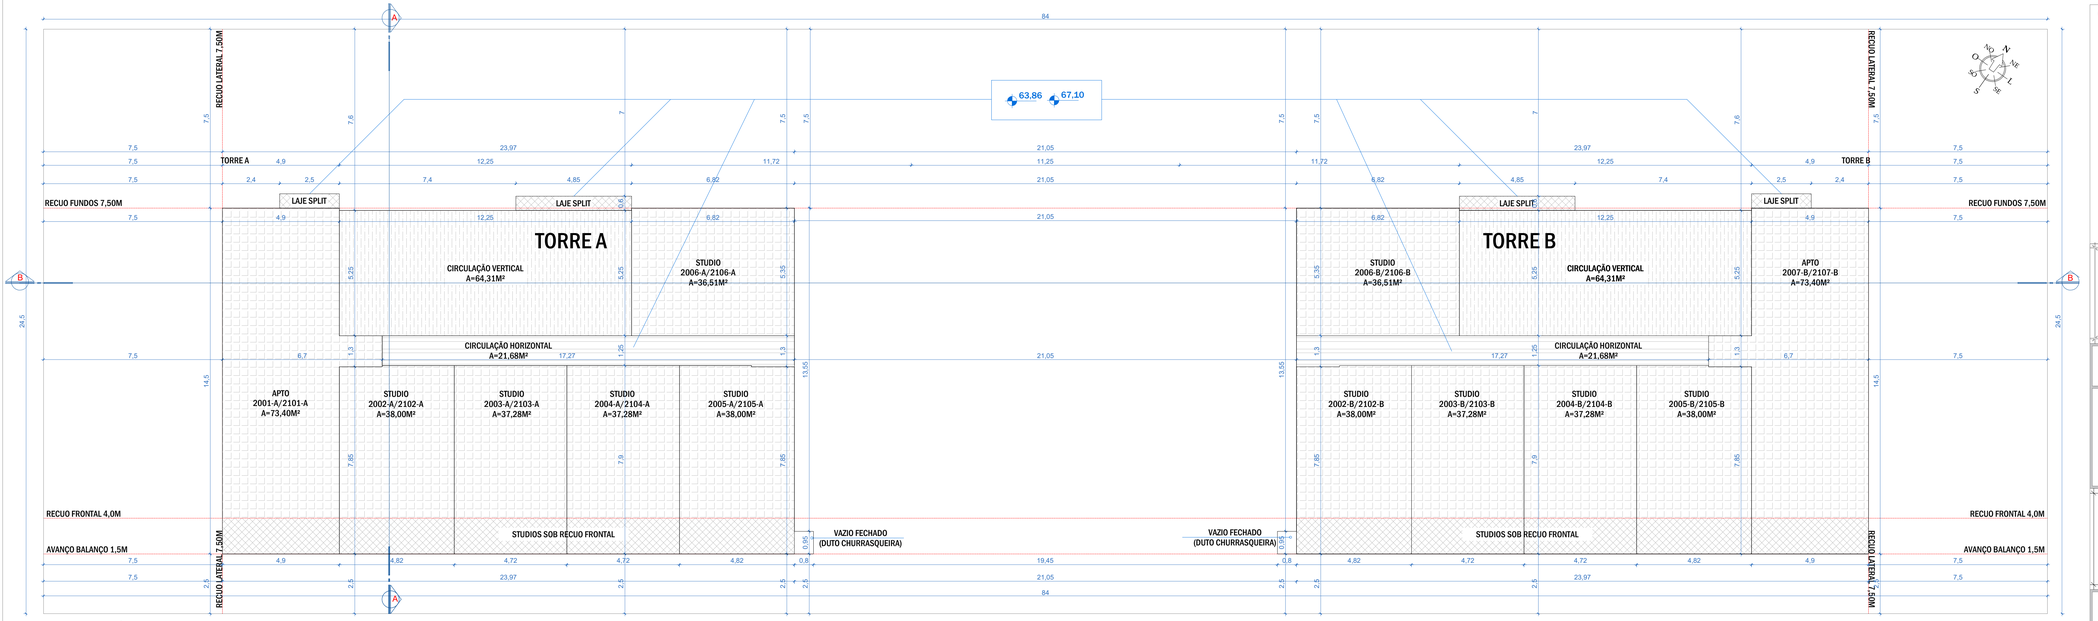

PLANTA PERÍMETRO - 20°/21° PAVIMENTO - TIPO 03 X02

ESCALA 1/100

LEGENDA

- UNIDADES RESIDENCIAIS
- UNIDADES COMERCIAIS
- LAZER COBERTO
- LAZER DESCOBERTO
- LAZER ABERTO COBERTO
- CIRCULAÇÃO VERTICAL
- CIRCULAÇÃO HORIZONTAL
- ÁREA DE USO COMUM
- COBERTURA (SEM USO)
- RESERVATÓRIO
- RAMPA
- EMBASAMENTO
- PROJ.DA EDIF.
- ÁREA PERMEÁVEL
- ELEMENTO CONSTRUTIVO PROJETADO SOBRE O RECUO FRONTAL/AFASTAMENTOS
- CIRCULAÇÃO ELEVADA
- AREA ACESSO PÚBLICO

CARIMBOS PREFEITURA

Assinado digitalmente por: LUIS ANDRE RIOS 098.375.269-52 05/10/2026 13:23:33

ESTE DOCUMENTO FOI ASSINADO DIGITALMENTE POR LUIS ANDRE RIOS:09837526952 E POR AUTENTICAR:00000000000 EM 05/10/2026 13:23:33
Acesse https://autenticar.itajai.sc.gov.br/autenticidade com o código 00000000

MV PROJETOS

ENGENHARIA - ARQUITETURA
CONSULTORIA TÉCNICA
RUA ANTÔNIO ZEFERINO STEIN - Nº 97
PEREQUÊ , PORTO BELO - SC/ CEP 88210-000, TEL: (47) 99923-3201
mvprojetosportobelo@gmail.com

PROJETO ARQUITETÔNICO

PORTO BELO FÁCIL

RESPONSÁVEL TÉCNICO:

gov.br Documento assinado digitalmente JESSICA MUNHOZ VIEIRA Data: 10/09/2026 16:53:47-0300 Verifique em https://validar.iti.gov.br

ARQ° JESSICA MUNHOZ VIEIRA
CAU-SC A321019-7

PROPRIETÁRIO:

MAXCES CONSTRUTORA E INCORPORADORA LTDA:33542372000107 Assinado de forma digital por MAXCES CONSTRUTORA E INCORPORADORA LTDA:33542372000107 Dados: 2026.09.10 13:05:40 -03'00'

MAXCES CONSTRUTORA E INCORPORADORA LTDA
CNPJ: 33.542.372/0001-07

DENOMINAÇÃO:

EDIFICAÇÃO RESIDENCIAL MULTIFAMILIAR E COMERCIAL
CONECTA TOWERS

ENDEREÇO:


AVENIDA VEREADOR PEDRO ELIAS RODRIGUES, n° 1600, LOTEAMENTO JARDIM DOURADO, BAIRRO ALTO PEREQUE - PORTO BELO - SC

CONTEÚDO:

PLANTA PERÍMETRO - 19º PAVIMENTO - TIPO 02 X 01
PLANTA PERÍMETRO - 20º / 21º PAVIMENTO - TIPO 03 X 02


FOLHA **05/11**

ESCALA:	DATA:	DESENHO TÉCNICO:	REVISÃO:
INDICADA	SET/2026	JESSICA MUNHOZ VIEIRA	02

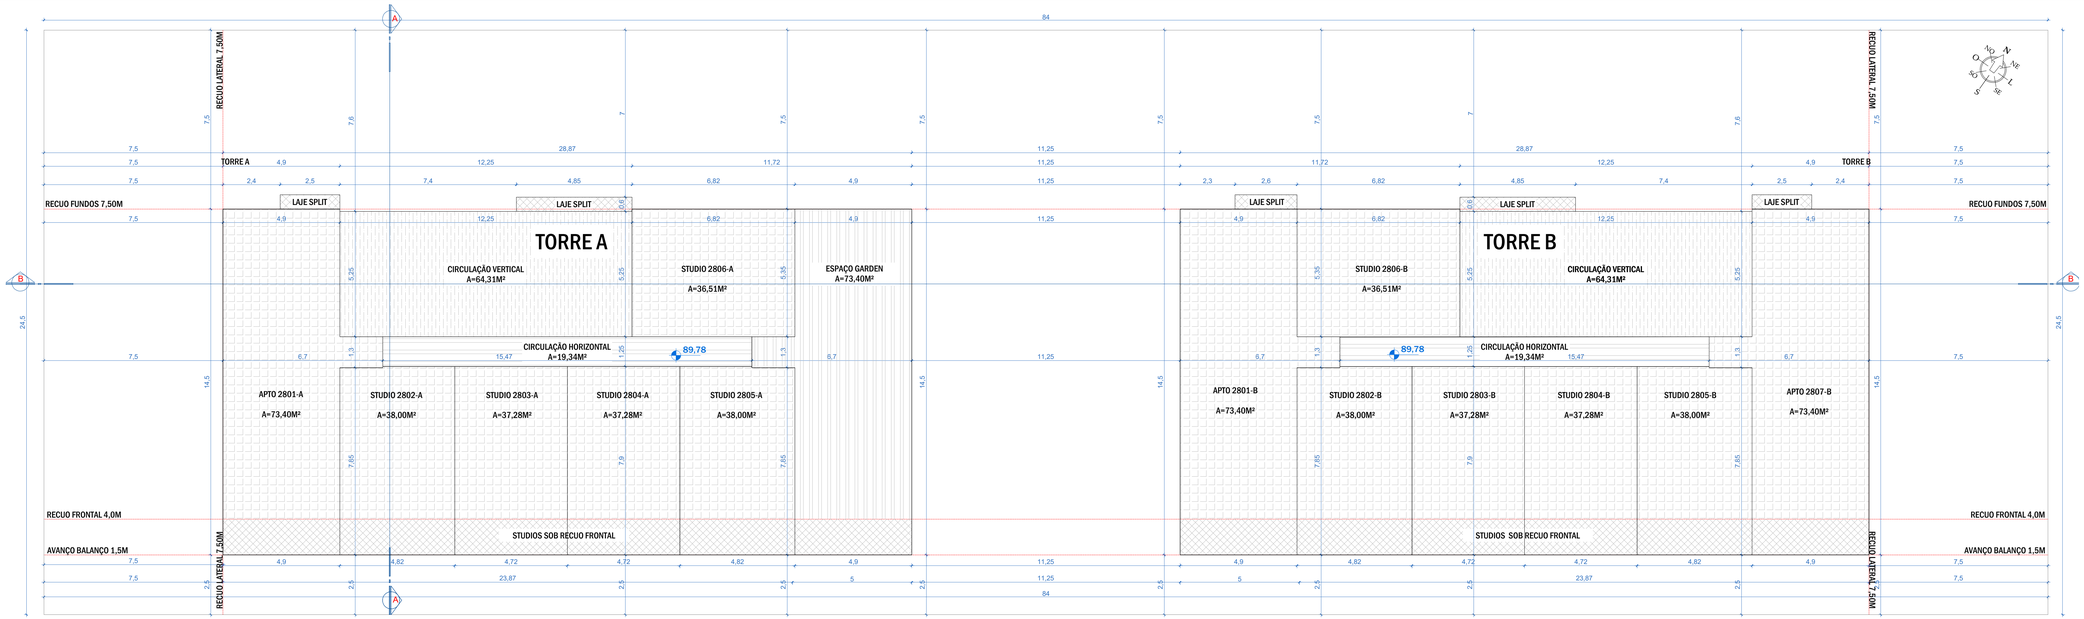

PLANTA PERÍMETRO - 28° PAVIMENTO - TIPO 04 X 01

ESCALA 1/100

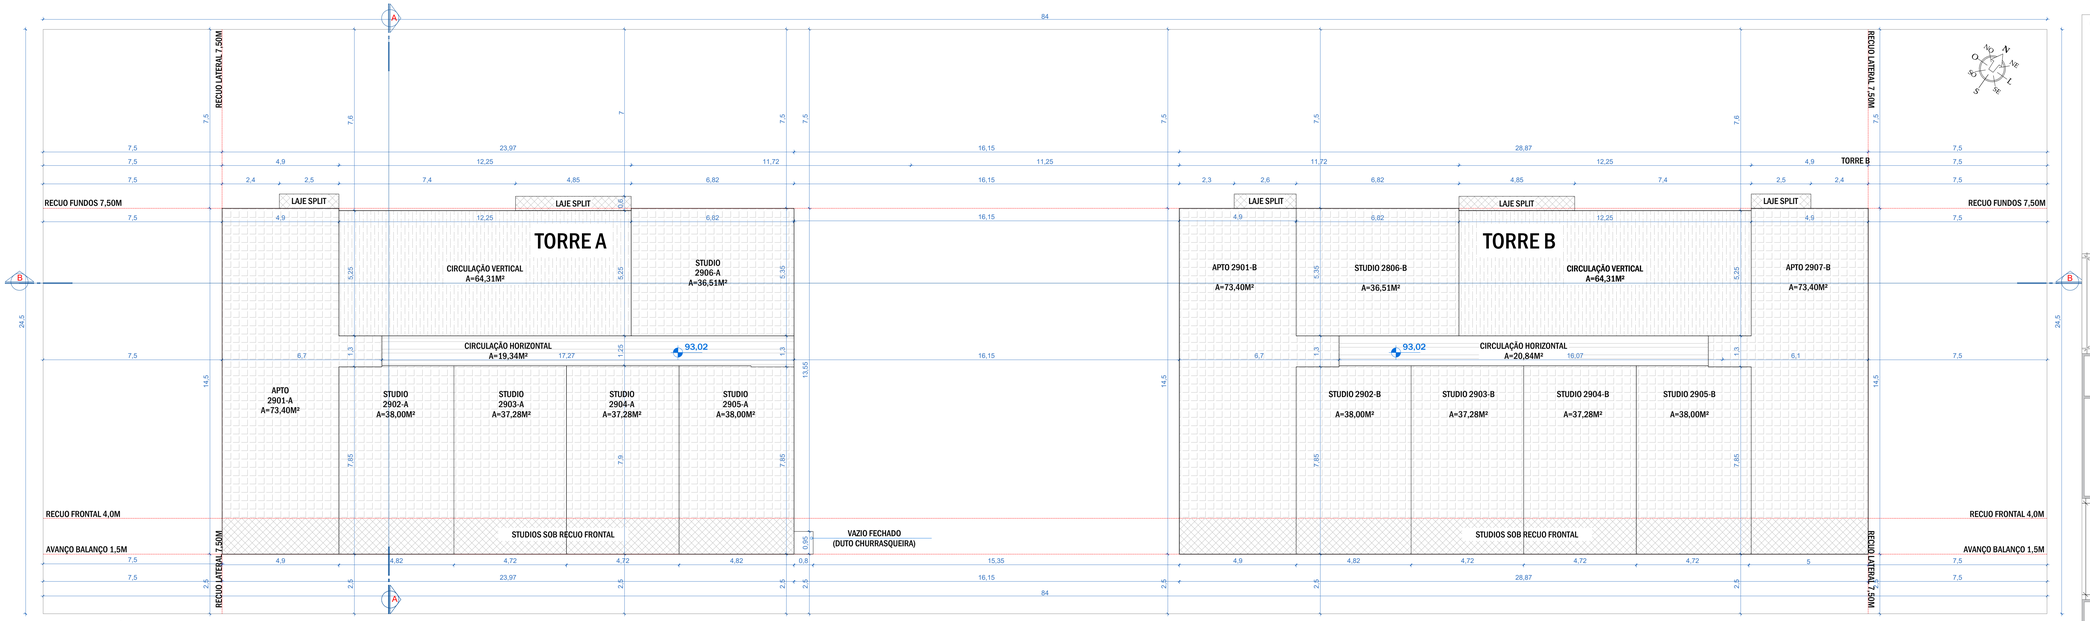

PLANTA PERÍMETRO - 29° PAVIMENTO - TIPO 05 X 01

ESCALA 1/100

LEGENDA

- UNIDADES RESIDENCIAIS
- UNIDADES COMERCIAIS
- LAZER COBERTO
- LAZER DESCOBERTO
- LAZER ABERTO COBERTO
- CIRCULAÇÃO VERTICAL
- CIRCULAÇÃO HORIZONTAL
- ÁREA DE USO COMUM
- COBERTURA (SEM USO)
- RESERVATÓRIO
- RAMPA
- EMBASAMENTO
- PROJ.DA EDIF.
- ÁREA PERMEÁVEL
- ELEMENTO CONSTRUTIVO PROJETADO SOBRE O RECUO FRONTAL/AFASTAMENTOS
- CIRCULAÇÃO ELEVADA
- AREA ACESSO PÚBLICO

CARIMBOS PREFEITURA

Assinado digitalmente por: LUIS ANDRE RIOS CPF: 071.265.419-45
assinado digitalmente 05/10/2026 13:23:43

ESTE DOCUMENTO FOI ASSINADO DIGITALMENTE POR LUIS ANDRE RIOS EM 05/10/2026 13:23:43
A AUTENTICIDADE DESTE DOCUMENTO PODE SER VERIFICADA NO SITE https://validar.iti.gov.br COM A CHAVE 2f0b4c3d1e5a6b7c8d9e0f1a2b3c4d5e6f7a8b9c

MV PROJETOS
ENGENHARIA - ARQUITETURA
CONSULTORIA TÉCNICA
RUA ANTÔNIO ZEFERINO STEIN - Nº 97
PEREQUÊ , PORTO BELO - SC/ CEP 88210-000, TEL: (47) 99923-3201
mvprojetosportobelo@gmail.com

PROJETO ARQUITETÔNICO

PORTO BELO FÁCIL

RESPONSÁVEL TÉCNICO:

gov.br Documento assinado digitalmente JESSICA MUNHOZ VIEIRA Data: 02/05/2026 16:53:47-0300 Verifique em https://validar.iti.gov.br

ARQ° JESSICA MUNHOZ VIEIRA
CAU-SC A321019-7

PROPRIETÁRIO:

MAXCES CONSTRUTORA E INCORPORADORA LTDA:33542372000107

Assinado de forma digital por MAXCES CONSTRUTORA E INCORPORADORA LTDA:33542372000107 Dados: 2026.04.10 13:06:33 -03'00'

MAXCES CONSTRUTORA E INCORPORADORA LTDA
CNPJ: 33.542.372/ 0001-07

DENOMINAÇÃO:

EDIFICAÇÃO RESIDENCIAL MULTIFAMILIAR E COMERCIAL
CONECTA TOWERS

ENDEREÇO:


AVENIDA VEREADOR PEDRO ELIAS RODRIGUES, n° 1600, LOTEAMENTO JARDIM DOURADO, BAIRRO ALTO PEREQUE - PORTO BELO - SC

CONTEÚDO:

PLANTA PERÍMETRO - 28° PAVIMENTO - TIPO 04X01
PLANTA PERÍMETRO - 29° PAVIMENTO - TIPO 05X01


FOLHA 06/11

ESCALA:	DATA:	DESENHO TÉCNICO:	REVISÃO:
INDICADA	SET/2026	JESSICA MUNHOZ VIEIRA	02

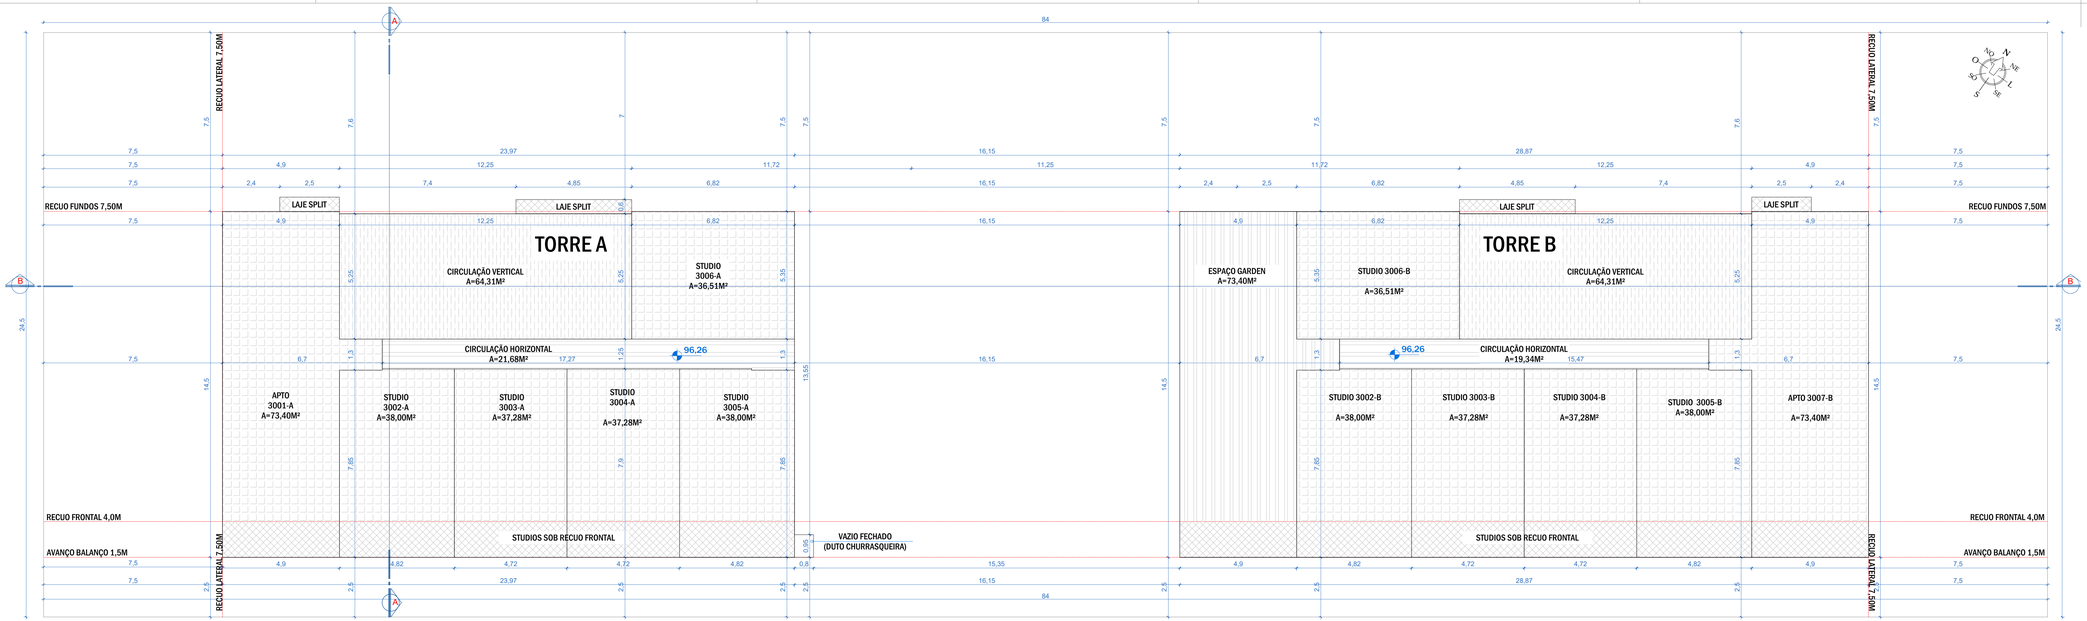

PLANTA PERÍMETRO - 30° PAVIMENTO - TIPO 06 X 01

ESCALA 1/100

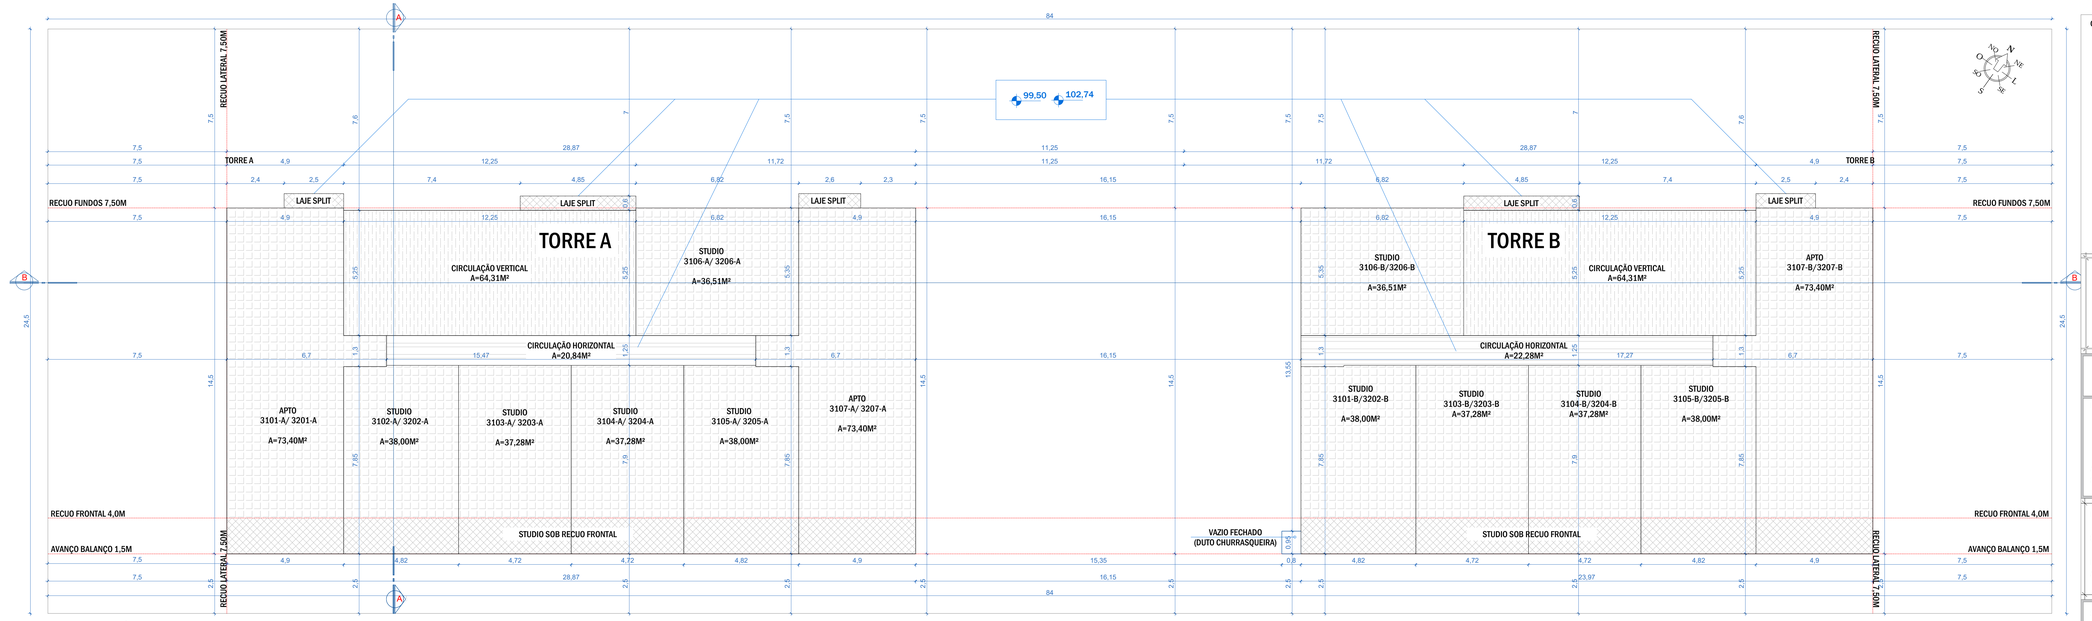

PLANTA PERÍMETRO - 31°/32° PAVIMENTO - TIPO 07 X 02

ESCALA 1/100

LEGENDA

- UNIDADES RESIDENCIAIS
- UNIDADES COMERCIAIS
- LAZER COBERTO
- LAZER DESCOBERTO
- LAZER ABERTO COBERTO
- CIRCULAÇÃO VERTICAL
- CIRCULAÇÃO HORIZONTAL
- ÁREA DE USO COMUM
- COBERTURA (SEM USO)
- RESERVATÓRIO
- RAMPA
- EMBASAMENTO
- PROJ.DA EDIF.
- ÁREA PERMEÁVEL
- ELEMENTO CONSTRUTIVO PROJETADO SOBRE O RECUO FRONTAL/AFASTAMENTOS
- CIRCULAÇÃO ELEVADA
- AREA ACESSO PÚBLICO

CARIMBOS PREFEITURA

Assinado digitalmente por: LUIS ANDRE RIOS SIMEAN:06964
assinado digitalmente 05/10/2026 13:23:53

ESTE DOCUMENTO FOI ASSINADO DIGITALMENTE POR LUIS ANDRE RIOS SIMEAN:06964 EM 05/10/2026 13:23:53 -03:00
VERIFIQUE ESTE DOCUMENTO EM HTTPS://VALIDAR.ITI.GOV.BR

MV PROJETOS
ENGENHARIA - ARQUITETURA
CONSULTORIA TÉCNICA
RUA ANTÔNIO ZEFERINO STEIN - Nº 97
PEREQUÊ , PORTO BELO - SC/ CEP 88210-000, TEL: (47) 99923-3201
mvprojetosportobelo@gmail.com

PROJETO ARQUITETÔNICO

PORTO BELO FÁCIL

RESPONSÁVEL TÉCNICO:

gov.br Documento assinado digitalmente JESSICA MUNHOZ VIEIRA Data: 10/09/2026 16:53:47-0300 Verifique em https://validar.iti.gov.br

ARQ° JESSICA MUNHOZ VIEIRA
CAU-SC A321019-7

PROPRIETÁRIO:

MAXCES CONSTRUTORA E INCORPORADORA LTDA:33542372000107 Assinado de forma digital por MAXCES CONSTRUTORA E INCORPORADORA LTDA:33542372000107 Dados: 2026.09.10 13:07:39 -03'00'

MAXCES CONSTRUTORA E INCORPORADORA LTDA
CNPJ: 33.542.372/0001-07

DENOMINAÇÃO:

EDIFICAÇÃO RESIDENCIAL MULTIFAMILIAR E COMERCIAL
CONECTA TOWERS

ENDEREÇO:

AVENIDA VEREADOR PEDRO ELIAS RODRIGUES, n° 1600, LOTEAMENTO JARDIM DOURADO, BAIRRO ALTO PEREQUE - PORTO BELO - SC


CONTEÚDO:

PLANTA PERÍMETRO - 30° PAVIMENTO - TIPO 06X01

PLANTA PERÍMETRO - 31°/32° PAVIMENTO - TIPO 07X02

FOLHA 07/11

ESCALA:	DATA:	DESENHO TÉCNICO:	REVISÃO:
INDICADA	SET/2026	JESSICA MUNHOZ VIEIRA	02

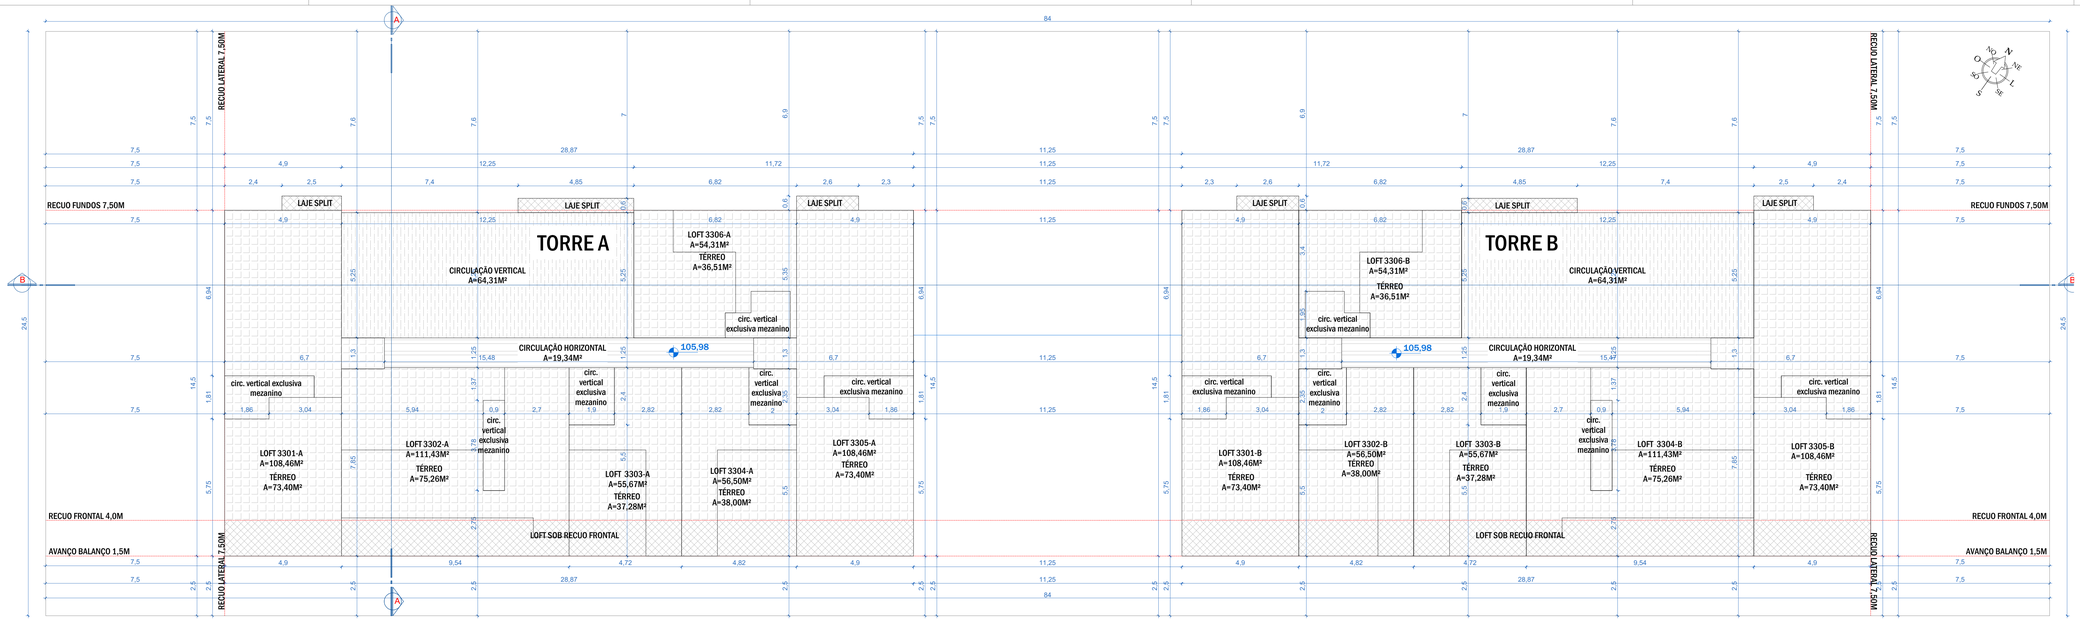


PLANTA PERÍMETRO - 33° PAVIMENTO - TIPO 08 (LOFT TÉRREO) X01

ESCALA 1/100

LEGENDA

- UNIDADES RESIDENCIAIS
- UNIDADES COMERCIAIS
- LAZER COBERTO
- LAZER DESCOBERTO
- LAZER ABERTO COBERTO
- CIRCULAÇÃO VERTICAL
- CIRCULAÇÃO HORIZONTAL
- ÁREA DE USO COMUM
- COBERTURA (SEM USO)
- RESERVATÓRIO
- RAMPA
- EMBASAMENTO
- PROJ.DA EDIF.
- ÁREA PERMEÁVEL
- ELEMENTO CONSTRUTIVO PROJETADO SOBRE O RECUO FRONTAL/AFASTAMENTOS
- CIRCULAÇÃO ELEVADA
- AREA ACESSO PÚBLICO

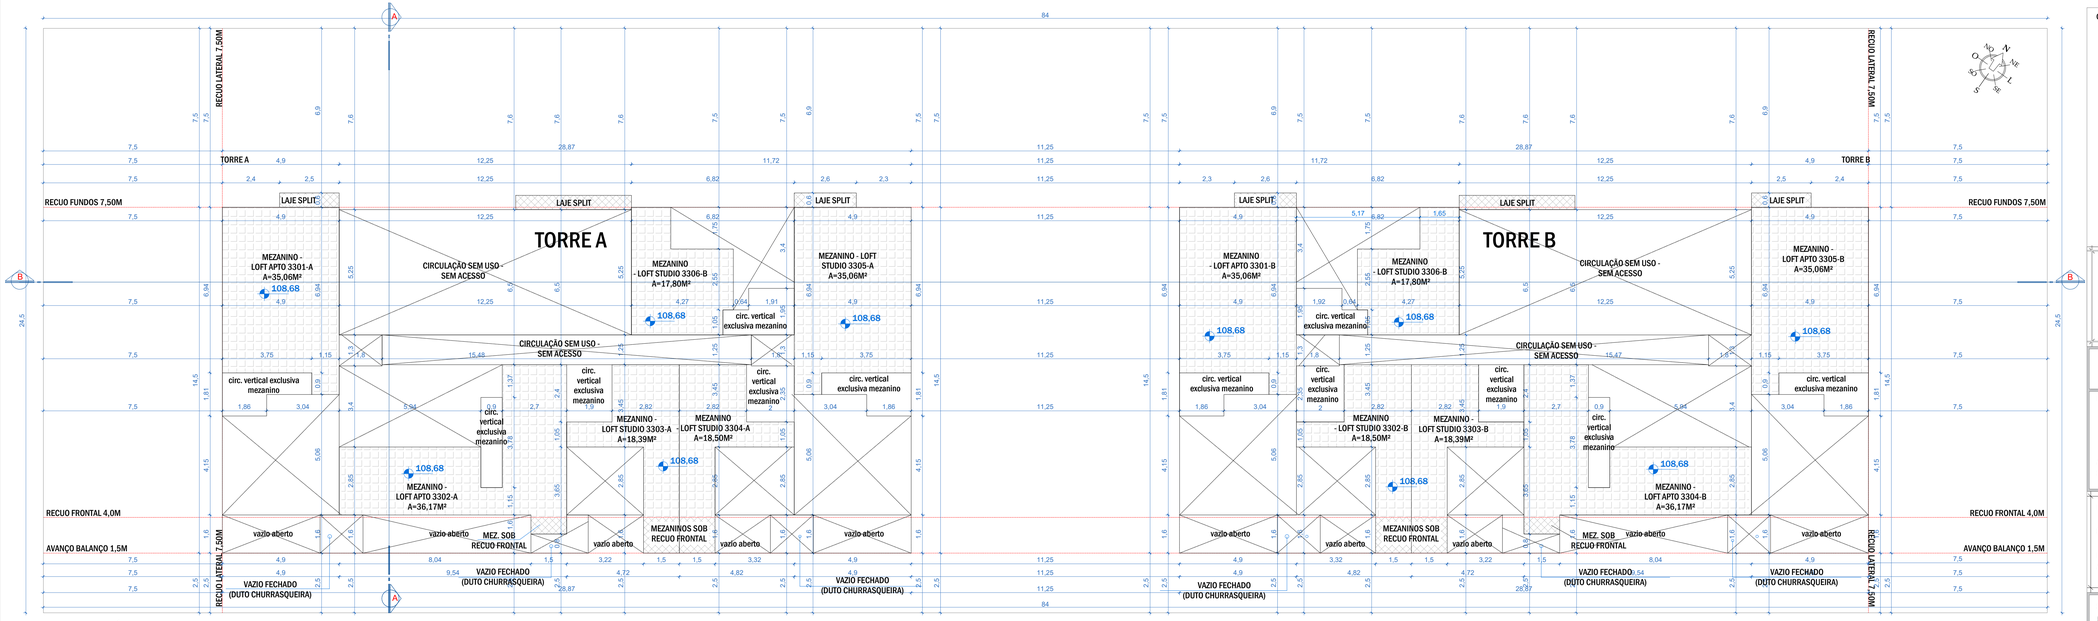

PLANTA PERÍMETRO - 33° PAVIMENTO - TIPO 08 (LOFT MEZANINO) X 01

ESCALA 1/100

CARIMBOS PREFEITURA

Assinado digitalmente por: LUIS ANDRE RIOS 098.375.269-52 05/10/2026 13:24:03

ESTE DOCUMENTO FOI ASSINADO DIGITALMENTE POR LUIS ANDRE RIOS EM 05/10/2026 13:24:03 -03:00
VERIFIQUE AUTENTICIDADE DO DOCUMENTO EM HTTPS://VALIDAR.IO.GOV.BR

MV PROJETOS
ENGENHARIA - ARQUITETURA
CONSULTORIA TÉCNICA
RUA ANTÔNIO ZEFERINO STEIN - Nº 97
PEREQUÊ , PORTO BELO - SC/ CEP 88210-000, TEL: (47) 99923-3201
mvprojetosportobelo@gmail.com

PROJETO ARQUITETÔNICO

PORTO BELO FÁCIL

RESPONSÁVEL TÉCNICO:

govbr Documento assinado digitalmente JESSICA MUNHOZ VIEIRA Data: 11/09/2026 08:19:52-0300 Verifique em https://validar.iti.gov.br

ARQ° JESSICA MUNHOZ VIEIRA
CAU-SC A321019-7

PROPRIETÁRIO:

MAXCES CONSTRUTORA E INCORPORADORA LTDA:33542372000107 Assinado de forma digital por MAXCES CONSTRUTORA E INCORPORADORA LTDA:33542372000107 Dados: 2026.09.10 13:08:36 -03'00'

MAXCES CONSTRUTORA E INCORPORADORA LTDA
CNPJ: 33.542.372/0001-07

DENOMINAÇÃO:

EDIFICAÇÃO RESIDENCIAL MULTIFAMILIAR E COMERCIAL
CONECTA TOWERS

ENDEREÇO:


AVENIDA VEREADOR PEDRO ELIAS RODRIGUES, n° 1600, LOTEAMENTO JARDIM DOURADO, BAIRRO ALTO PEREQUE - PORTO BELO - SC

CONTEÚDO:

PLANTA PERÍMETRO - 33° PAVIMENTO - TIPO 08 (LOFT TÉRREO) X01
PLANTA PERÍMETRO - 33° PAVIMENTO - TIPO 08 (LOFT MEZANINO) X01

FOLHA 08/11


ESCALA:	DATA:	DESENHO TÉCNICO:	REVISÃO:
INDICADA	SET/2026	JESSICA MUNHOZ VIEIRA	02

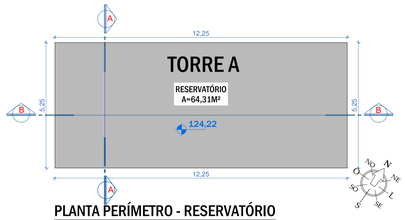


PLANTA PERÍMETRO - RESERVATÓRIO
ESCALA 1/100



PLANTA PERÍMETRO - RESERVATÓRIO
ESCALA 1/100

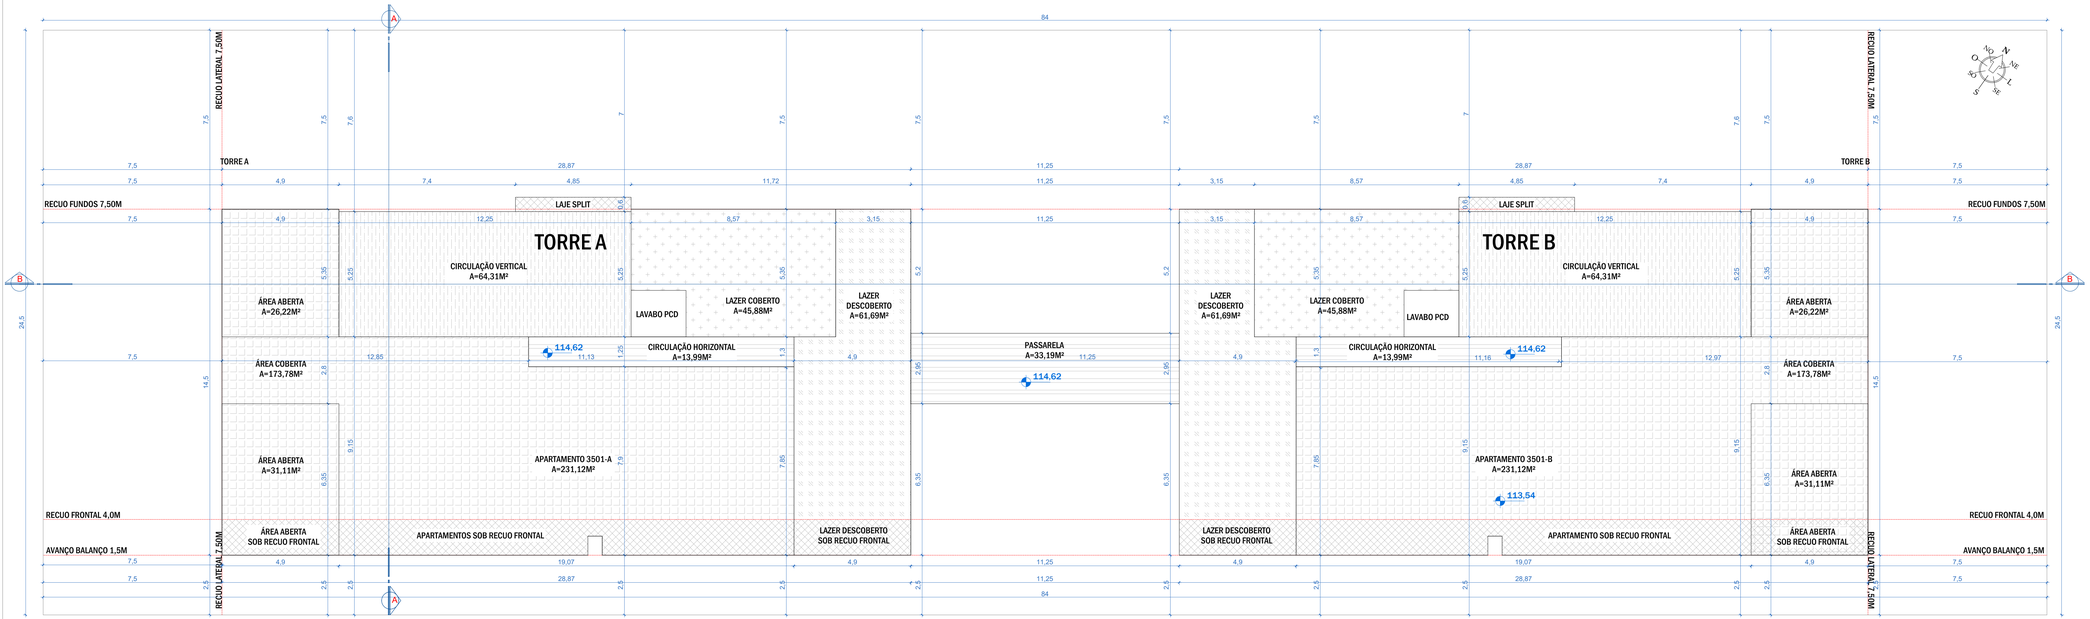

PLANTA PERÍMETRO - 35° PAVIMENTO - TIPO 09X01
ESCALA 1/100

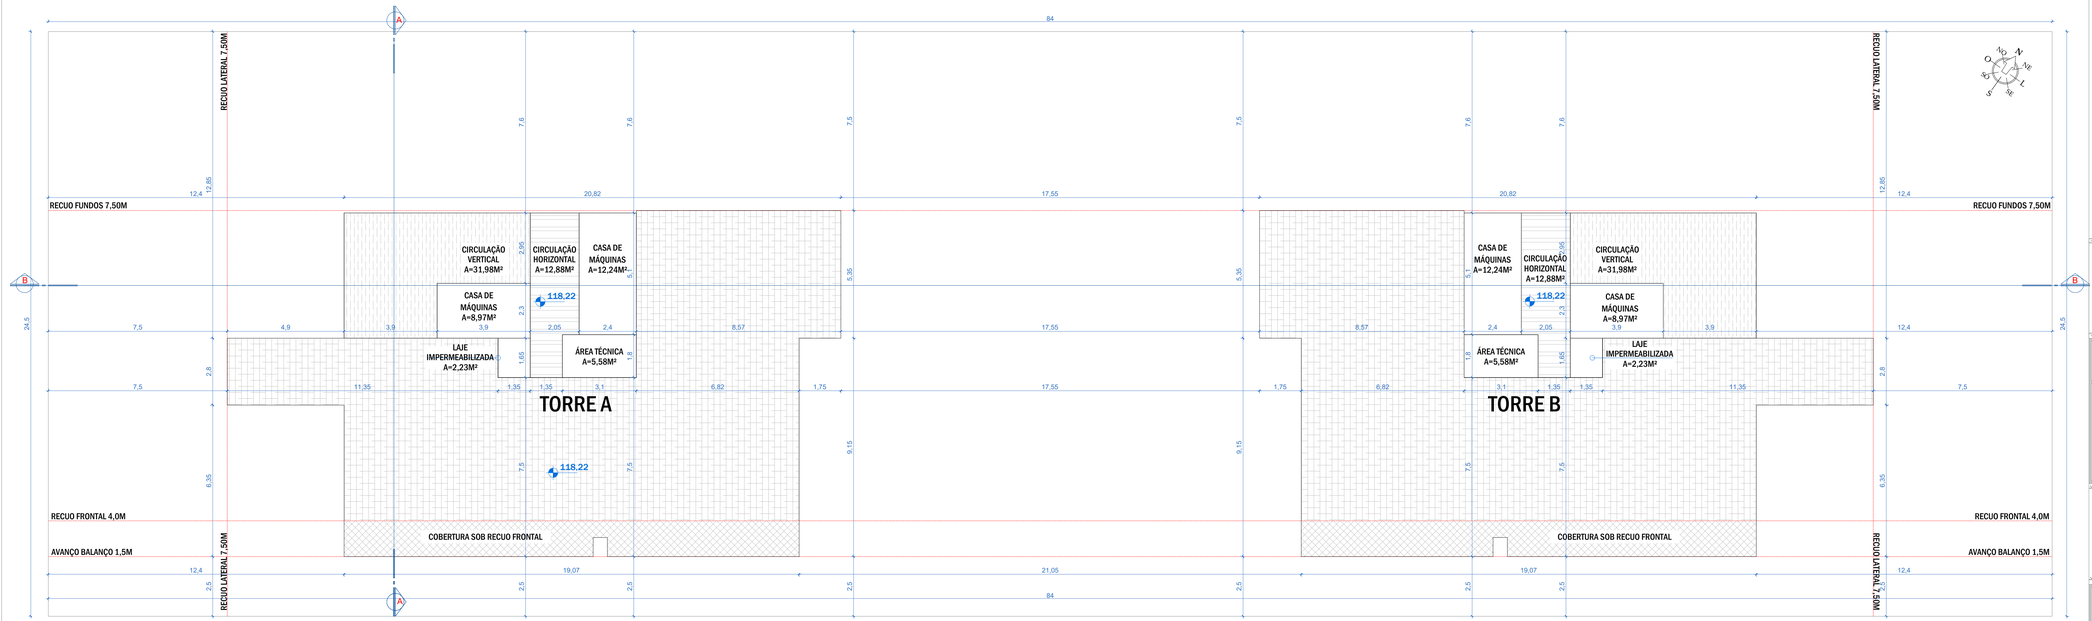

PLANTA PERÍMETRO - COBERTURA E BARRILETE
ESCALA 1/100

LEGENDA

- UNIDADES RESIDENCIAIS
- UNIDADES COMERCIAIS
- LAZER COBERTO
- LAZER DESCOBERTO
- LAZER ABERTO COBERTO
- CIRCULAÇÃO VERTICAL
- CIRCULAÇÃO HORIZONTAL
- ÁREA DE USO COMUM
- COBERTURA (SEM USO)
- RESERVATÓRIO
- RAMPA
- EMBASAMENTO
- PROJ.DA EDIF.
- ÁREA PERMEÁVEL
- ELEMENTO CONSTRUTIVO PROJETADO SOBRE O RECUO FRONTAL/AFASTAMENTOS
- CIRCULAÇÃO ELEVADA
- AREA ACESSO PÚBLICO

CARIMBOS PREFEITURA

Assinado digitalmente por: LUIS ANDRE RIOS
Data: 21/10/2026 13:24:15
assinado digitalmente

MV PROJETOS

ENGENHARIA - ARQUITETURA
CONSULTORIA TÉCNICA
RUA ANTÔNIO ZEFERINO STEIN - Nº 97
PEREQUÊ , PORTO BELO - SC/ CEP 88210-000, TEL: (47) 99923-3201
mvprojetosportobelo@gmail.com

PROJETO ARQUITETÔNICO

PORTO BELO FÁCIL

RESPONSÁVEL TÉCNICO:
Documento assinado digitalmente
gov.br JESSICA MUNHOZ VIEIRA
Data: 11/09/2026 08:16:48-0300
Verifique em https://validar.iti.gov.br

ARQ° JESSICA MUNHOZ VIEIRA
CAU-SC A321019-7

PROPRIETÁRIO:
MAXCES CONSTRUTORA E INCORPORADORA LTDA:33542372000107
Assinado de forma digital por MAXCES CONSTRUTORA E INCORPORADORA LTDA:33542372000107
Dados: 2026.09.10 13:09:27 -03'00'

MAXCES CONSTRUTORA E INCORPORADORA LTDA
CNPJ: 33.542.372/0001-07

DENOMINAÇÃO:
EDIFICAÇÃO RESIDENCIAL MULTIFAMILIAR E COMERCIAL
CONECTA TOWERS


ENDEREÇO:
AVENIDA VEREADOR PEDRO ELIAS RODRIGUES, n°1600, LOTEAMENTO JARDIM DOURADO, BAIRRO ALTO PEREQUE - PORTO BELO - SC

CONTEÚDO:
PLANTA PERÍMETRO - 35° PAVIMENTO - TIPO 09X01
PLANTA PERÍMETRO - COBERTURA/BARRILETE E RESERVATÓRIOS

FOLHA
09/11

ESCALA:	DATA:	DESENHO TÉCNICO:	REVISÃO:
INDICADA	SET/2026	JESSICA MUNHOZ VIEIRA	02

ESTE DOCUMENTO FOI ASSINADO DIGITALMENTE POR LUIS ANDRE RIOS E JESSICA MUNHOZ VIEIRA.
A AUTENTICIDADE DESTE DOCUMENTO PODE SER VERIFICADA NO SITE https://validar.iti.gov.br

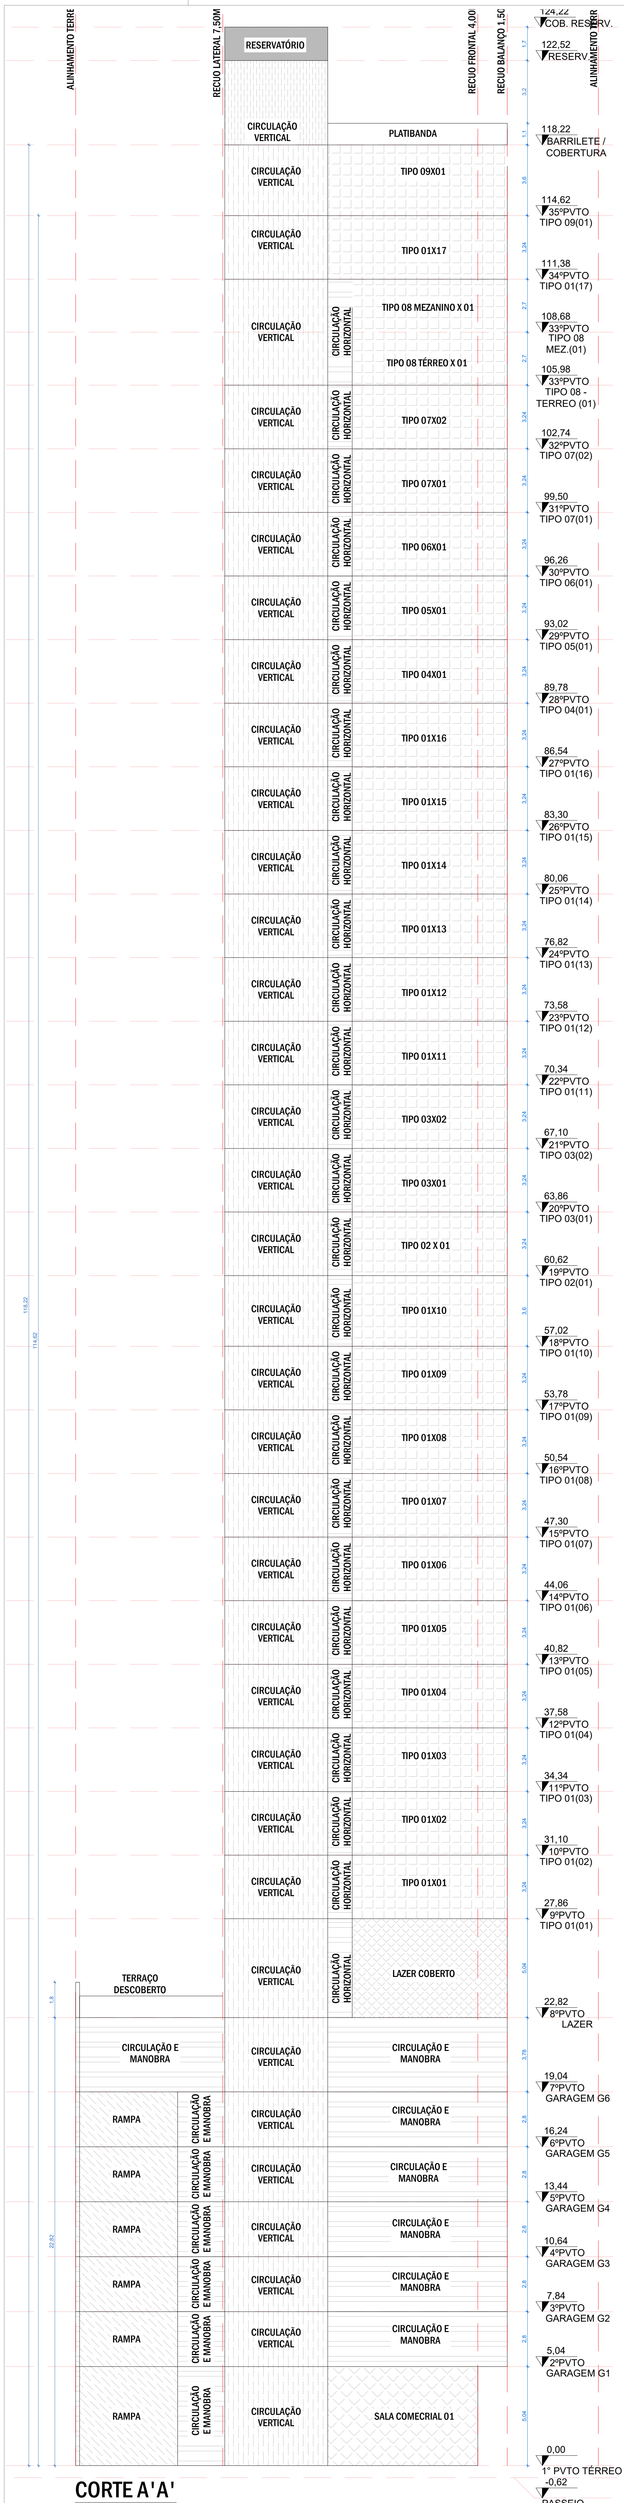

CORTE A'A'
ESCALA 1/125

LEGENDA

- UNIDADES RESIDENCIAIS
- UNIDADES COMERCIAIS
- LAZER COBERTO
- LAZER DESCOBERTO
- LAZER ABERTO COBERTO
- CIRCULAÇÃO VERTICAL
- CIRCULAÇÃO HORIZONTAL
- ÁREA DE USO COMUM
- COBERTURA (SEM USO)
- RESERVATÓRIO
- RAMPA
- EMBASAMENTO
- PROJ.DA EDIF.
- ÁREA PERMEÁVEL
- ELEMENTO CONSTRUTIVO PROJETADO SOBRE O RECUO FRONTAL/AFASTAMENTOS
- CIRCULAÇÃO ELEVADA
- AREA ACESSO PÚBLICO

CARIMBOS PREFEITURA

Assinado digitalmente por: LUIS ANDRÉ RIOS 098.275.269-52 05/10/2026 13:24:25

ENGENHARIA - ARQUITETURA
CONSULTORIA TÉCNICA
RUA ANTÔNIO ZEFERINO STEIN - Nº 97
PEREQUÊ , PORTO BELO - SC/ CEP 88210-000, TEL: (47) 99923-3201
mvprojetosportobelo@gmail.com

PROJETO ARQUITETÔNICO

PORTO BELO FÁCIL

RESPONSÁVEL TÉCNICO:
Documento assinado digitalmente gov.br JESSICA MUNHOZ VIEIRA Data: 11/09/2024 08:16:48-0300 Verifique em https://validar.iti.gov.br
ARQ° JESSICA MUNHOZ VIEIRA
CAU-SC A321019-7

PROPRIETÁRIO:
MAXCES CONSTRUTORA E INCORPORADORA LTDA:33542372000107
Assinado de forma digital por MAXCES CONSTRUTORA E INCORPORADORA LTDA:33542372000107 Dados: 2024.09.19 13:16:23 -03'00'
MAXCES CONSTRUTORA E INCORPORADORA LTDA
CNPJ: 33.542.372/0001-07

DENOMINAÇÃO:
EDIFICAÇÃO RESIDENCIAL MULTIFAMILIAR E COMERCIAL
CONECTA TOWERS


ENDEREÇO:
AVENIDA VEREADOR PEDRO ELIAS RODRIGUES, n° 1600, LOTEAMENTO JARDIM DOURADO, BAIRRO ALTO PEREQUE - PORTO BELO - SC

CONTEÚDO:
CORTE A'A'

FOLHA
10 /11

ESCALA:	DATA:	DESENHO TÉCNICO:	REVISÃO:
INDICADA	SET/2026	JESSICA MUNHOZ VIEIRA	02

ESTE DOCUMENTO FOI ASSINADO EM 05/10/2026 13:24:43 (H) 49
PARA CONFERÊNCIA ACESSE O SEU CONTEÚDO ACESSE: https://c-sim.com.br/validar/daa2365

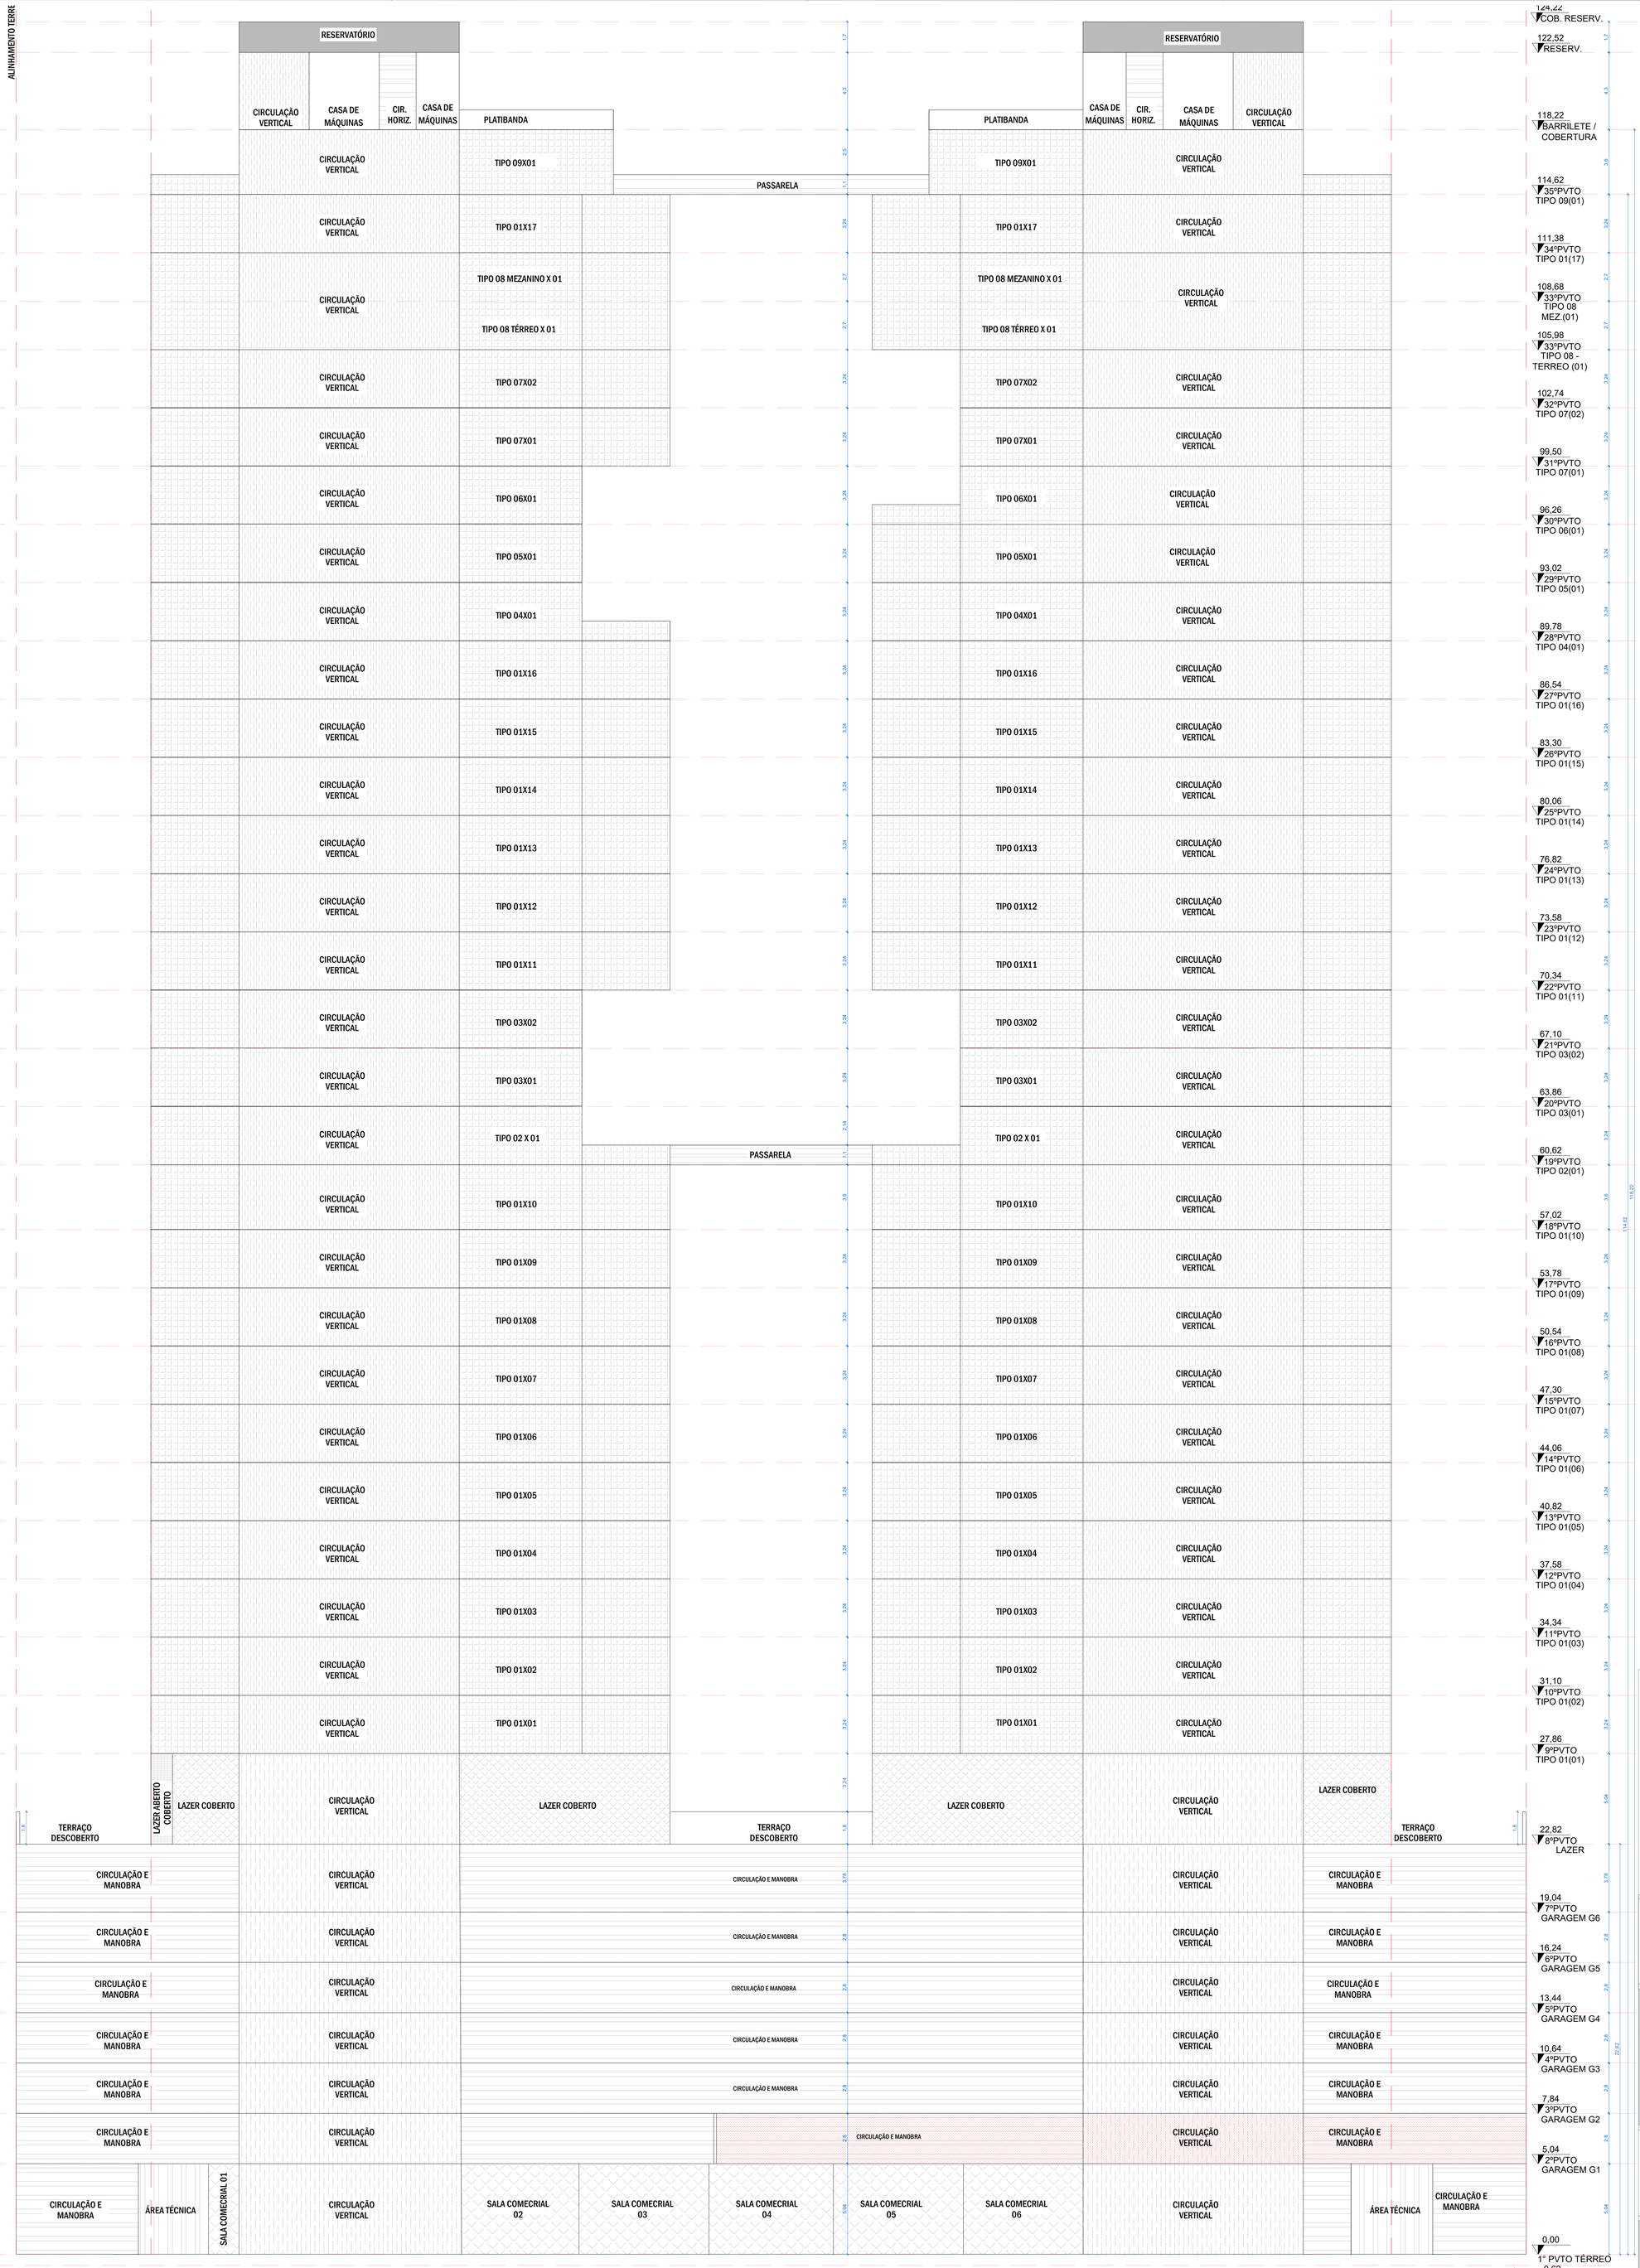

CORTE B'B'

ESCALA 1/125

LEGENDA

- UNIDADES RESIDENCIAIS
- UNIDADES COMERCIAIS
- LAZER COBERTO
- LAZER DESCOBERTO
- LAZER ABERTO COBERTO
- CIRCULAÇÃO VERTICAL
- CIRCULAÇÃO HORIZONTAL
- ÁREA DE USO COMUM
- COBERTURA (SEM USO)
- RESERVATÓRIO
- RAMPA
- EMBASAMENTO
- PROJ.DA EDIF.
- ÁREA PERMEÁVEL
- ELEMENTO CONSTRUTIVO PROJETADO SOBRE O RECUO FRONTAL/AFASTAMENTOS
- CIRCULAÇÃO ELEVADA
- AREA ACESSO PÚBLICO

CARIMBOS PREFEITURA

Assinado digitalmente por: LUIS ANDRE RIOS 098.275.269-52 assinado digitalmente 05/10/2026 13:24:39

ESTE DOCUMENTO FOI ASSINADO EM 06/10/2026 13:24:49 -03 POR LUIS ANDRE RIOS (098.275.269-52) VIA BRY Technology Solution.
https://prefeituraportobelo.1doc.com.br/verificacao/3A46-0A0E-3A5F-2AA6

MV PROJETOS
ENGENHARIA - ARQUITETURA
CONSULTORIA TÉCNICA
RUA ANTÔNIO ZEFERINO STEIN - Nº 97
PEREQUÊ , PORTO BELO - SC/ CEP 88210-000, TEL: (47) 99923-3201
mvprojetosportobelo@gmail.com

PROJETO ARQUITETÔNICO

PORTO BELO FÁCIL

RESPONSÁVEL TÉCNICO:
gov.br Documento assinado digitalmente JESSICA MUNHOZ VIEIRA Data: 11/09/2026 08:16:48-0300 Verifique em https://validar.iti.gov.br
ARQ° JESSICA MUNHOZ VIEIRA
CAU-SC A321019-7

PROPRIETÁRIO:
MAXCES CONSTRUTORA E INCORPORADORA LTDA:33542372000107 Assinado de forma digital por MAXCES CONSTRUTORA E INCORPORADORA LTDA:33542372000107 Dados: 2026.09.10 11:11:25 -03'00'
MAXCES CONSTRUTORA E INCORPORADORA LTDA
CNPJ: 33.542.372/0001-07

DENOMINAÇÃO:
EDIFICAÇÃO RESIDENCIAL MULTIFAMILIAR E COMERCIAL
CONECTA TOWERS

ENDEREÇO:
AVENIDA VEREADOR PEDRO ELIAS RODRIGUES, nº1600, LOTEAMENTO JARDIM DOURADO, BAIRRO ALTO PEREQUE - PORTO BELO - SC

CONTEÚDO:
CORTE B'B'

FOLHA
11 /11

ESCALA:	DATA:	DESENHO TÉCNICO:	REVISÃO:
INDICADA	SET/2026	JESSICA MUNHOZ VIEIRA	02